
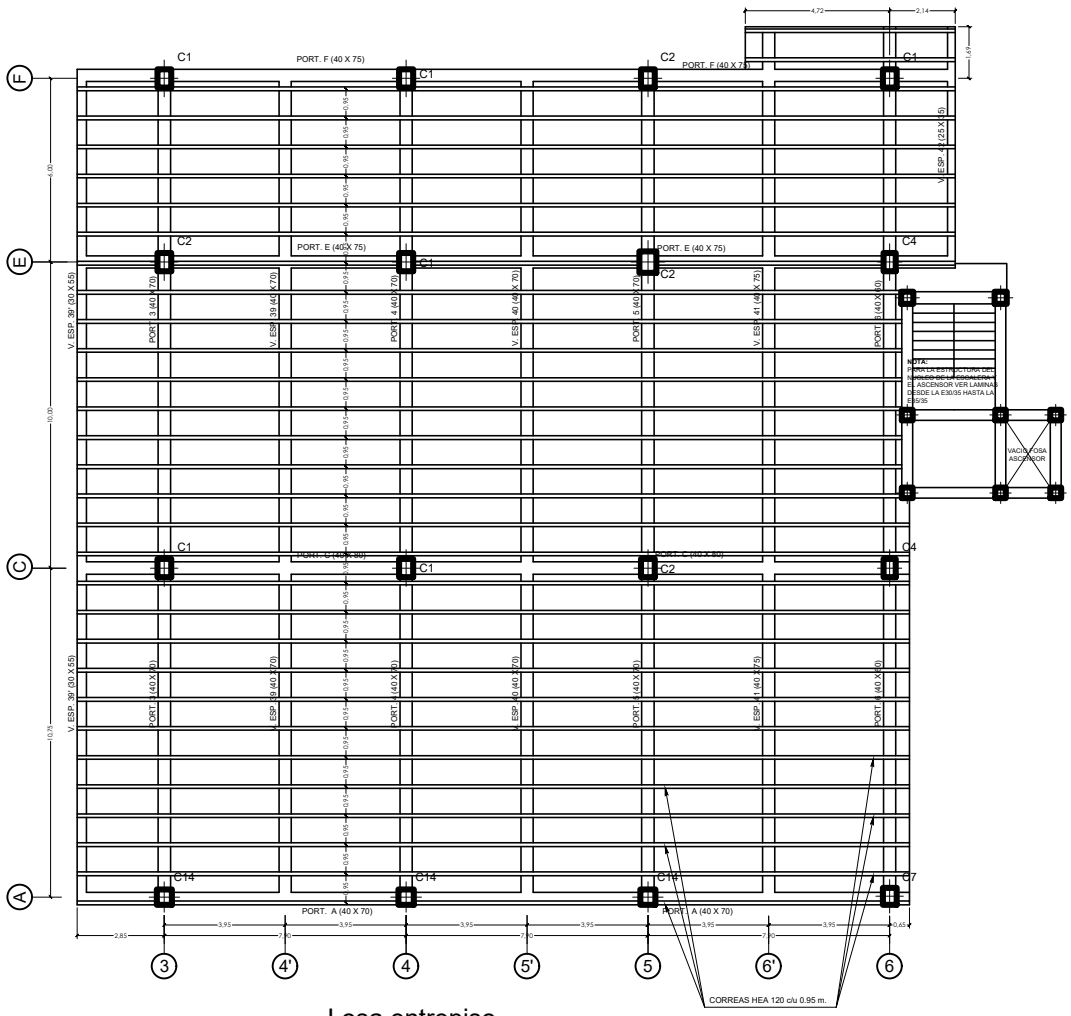


Losa entrepiso Loseta e = 10 cms. Esc. 1: 75


NIVEL (+11.60) (3° PISO) (N3)

CORREAS HEA 120 c /u 0.95m

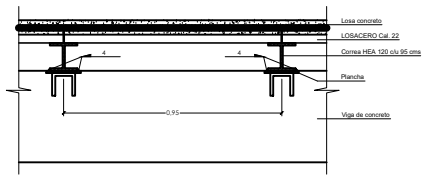


FIJACION LOSACERO ESC. 1:10

Espesor = 10 cms

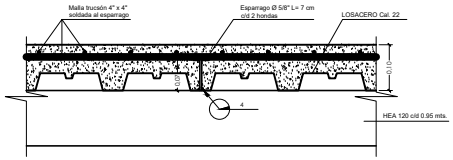

DETALLE LOSACERO ENTREPISO ESC. 1:5


Espesor = 10 cms

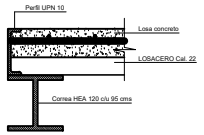

REMATE LATERAL ESC. 1:5

LOSACERO PLANTA BAJA, 1°, 2° y 3° PISO

Espesor = 10 cm, con esparrago Ø 5/8" L = 7 cm.

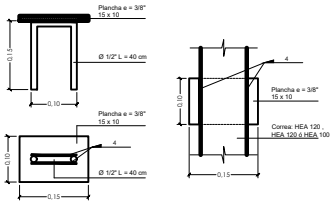

DETALLE PLANCHA ESC. 1:5

Gregorio H. Garzón Jaimes
PROPIETARIO
C.I. 9.218.667

Luz Marina Casanova J.
ARQUITECTO
C.I. 9.253.680 C.I.V. 95.596

Genaín Vivas Rosa
INGENIERO
C.I. 9.207.769 C.I.V. 71.525

PROYECTO: SUPERMERCADO EXPRESS Y OFICINAS CORPORATIVAS

PROPIETARIO: GARZÓN HIPERMERCADO C.A.
UBICACIÓN: AV. PUEBLO NUEVO ANACO EDO. ANZOATEGUI
ARQUITECTO: LUZ MARINA CASANOVA C.I.V. 95.596
DIBUJO: OTD

CONTENIDO: ESTRUCTURA ENTREPISO 3° PISO (NIVEL + 11.60 (N3)
N° CATASTRAL: 2023.04.10.10.007.01.000000.000
FECHA: MARZO 2011
ESCALA: 1/75

N. DE HOJA:
E-10/36

Garzón