V. ESP 41 (N3) (40 X 75) (3° PISO)

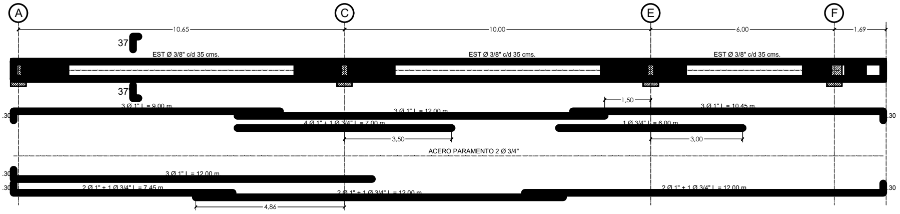
A
C
E
F
10.65
10,00
6,00
1,69
37
EST Ø 3/8" c/d 35 cms.
EST Ø 3/8" c/d 35 cms.
EST Ø 3/8" c/d 35 cms.
37'
3 Ø 1" L = 9.00 m
3 Ø 1" L = 12.00 m
1,50
3 Ø 1" L = 10.45 m
4 Ø 1" + 1 Ø 3/4" L = 7.00 m
1 Ø 3/4" L = 6.00 m
3,50
3,00
ACERO PARAMENTO 2 Ø 3/4"
3 Ø 1" L = 12.00 m
2 Ø 1" + 1 Ø 3/4" L = 7.45 m
2 Ø 1" + 1 Ø 3/4" L = 12.00 m
2 Ø 1" + 1 Ø 3/4" L = 12.00 m
4,86
.30

V. ESP 42 (N3) (25 X 35) (3° PISO)

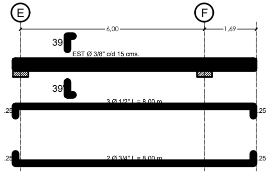
E
F
6,00
1,69
39
EST Ø 3/8" c/d 15 cms.
39'
3 Ø 1/2" L = 8.00 m
2 Ø 3/4" L = 8.00 m
.25

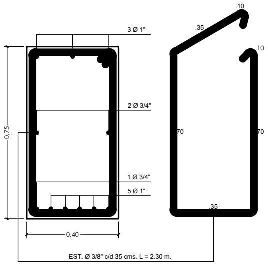
3 Ø 1"
2 Ø 3/4"
1 Ø 3/4"
5 Ø 1"
0,75
0,40
.35
.10
.70
EST. Ø 3/8" c/d 35 cms. L = 2.30 m.

CORTE 37-37' ESC. 1:10

V. ESP 43 = V. ESP. 44 = V. ESP. 45 (NT) (40 X 60) (TECHO)

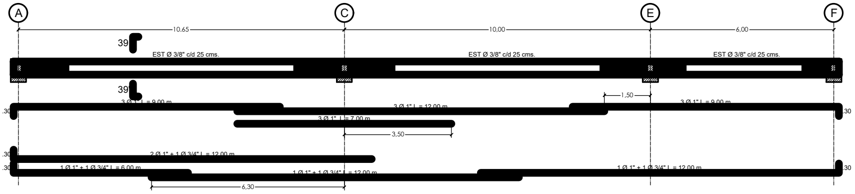
A
C
E
F
10.65
10,00
6,00
39
EST Ø 3/8" c/d 25 cms.
EST Ø 3/8" c/d 25 cms.
EST Ø 3/8" c/d 25 cms.
39'
3 Ø 1" L = 9.00 m
3 Ø 1" L = 12.00 m
1,50
3 Ø 1" L = 9.00 m
3 Ø 1" L = 7.00 m
3,50
2 Ø 1" + 1 Ø 3/4" L = 12.00 m
1 Ø 1" + 1 Ø 3/4" L = 6.00 m
1 Ø 1" + 1 Ø 3/4" L = 12.00 m
1 Ø 1" + 1 Ø 3/4" L = 12.00 m
6,30
.30

V. ESP 43' (NT) (30 X 45) (TECHO)

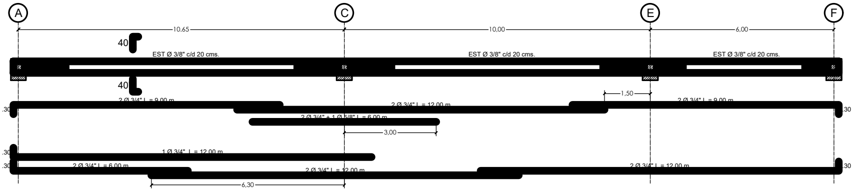
A
C
E
F
10.65
10,00
6,00
40
EST Ø 3/8" c/d 20 cms.
EST Ø 3/8" c/d 20 cms.
EST Ø 3/8" c/d 20 cms.
40'
2 Ø 3/4" L = 9.00 m
2 Ø 3/4" L = 12.00 m
1,50
2 Ø 3/4" L = 9.00 m
2 Ø 3/4" + 1 Ø 5/8" L = 6.00 m
3,00
1 Ø 3/4" L = 12.00 m
2 Ø 3/4" L = 6.00 m
2 Ø 3/4" L = 12.00 m
2 Ø 3/4" L = 12.00 m
6,30
.30

V. ESP 49 (S1) (55 X 80) (SOTANO 1)
(RAMPA ENTRE LOS SOTANOS)

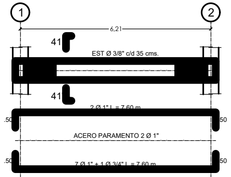
1
2
6,21
41
EST Ø 3/8" c/d 35 cms.
41'
2 Ø 1" L = 7.60 m
ACERO PARAMENTO 2 Ø 1"
7 Ø 1" + 1 Ø 3/4" L = 7.60 m
.50

V. ESP 50 (S1) (55 X 85) (SOTANO 1)
(RAMPA ENTRE LOS SOTANOS)

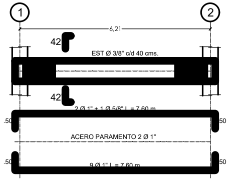
1
2
6,21
42
EST Ø 3/8" c/d 40 cms.
42'
2 Ø 1" + 1 Ø 5/8" L = 7.60 m
ACERO PARAMENTO 2 Ø 1"
9 Ø 1" L = 7.60 m
.50

V. ESP 51 (S1) (55 X 85) (SOTANO 1)
(RAMPA ENTRE LOS SOTANOS)

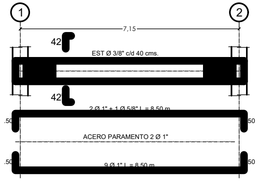
1
2
7,15
42
EST Ø 3/8" c/d 40 cms.
42'
2 Ø 1" + 1 Ø 5/8" L = 8.50 m
ACERO PARAMENTO 2 Ø 1"
9 Ø 1" L = 8.50 m
.50

V. VOL 01 = V. VOL. 03
(PB) (25 X 30)
(PLANTA BAJA)
(RAMPA PEATONAL)

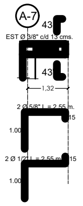
A-7
43
EST Ø 3/8" c/d 13 cms.
43'
1,32
2 Ø 5/8" L = 2.55 m.
2 Ø 1/2" L = 2.55 m
1.00
.15

V. VOL 02 (PB) (25 X 30)
(PLANTA BAJA)
(RAMPA PEATONAL)

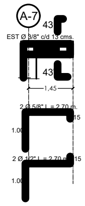
A-7
43
EST Ø 3/8" c/d 13 cms.
43'
1,45
2 Ø 5/8" L = 2.70 m.
2 Ø 1/2" L = 2.70 m
1.00
.15

V. APOY. DES. ESC.
(PB) (25 X 25)
(PLANTA BAJA)

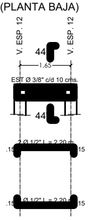
V. ESP. 12
V. ESP. 12
44
1,65
EST Ø 3/8" c/d 10 cms.
44'
2 Ø 1/2" L = 2.20 m
2 Ø 1/2" L = 2.20 m
.15

V. EJE 7' = V. EJE 19' (30 X 35)
(TECHO CUARTO BASURA)

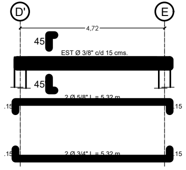
D'
E
4,72
45
EST Ø 3/8" c/d 15 cms.
45'
2 Ø 5/8" L = 5.32 m
2 Ø 3/4" L = 5.32 m
.15

V. AMARRE (30 X 30)
(TECHO CUARTO BASURA)

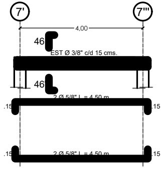
7'
7'''
4,00
46
EST Ø 3/8" c/d 15 cms.
46'
2 Ø 5/8" L = 4.50 m
2 Ø 5/8" L = 4.50 m
.15

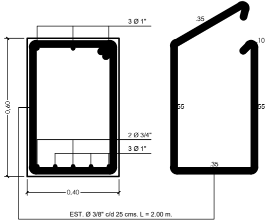
3 Ø 1"
2 Ø 3/4"
3 Ø 1"
0,60
0,40
.35
.10
.55
EST. Ø 3/8" c/d 25 cms. L = 2.00 m.

CORTE 39-39' ESC. 1:10

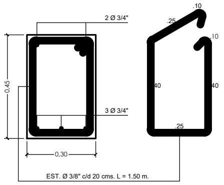
2 Ø 3/4"
3 Ø 3/4"
0,45
0,30
.25
.10
.40
EST. Ø 3/8" c/d 20 cms. L = 1.50 m.

CORTE 40-40' ESC. 1:10

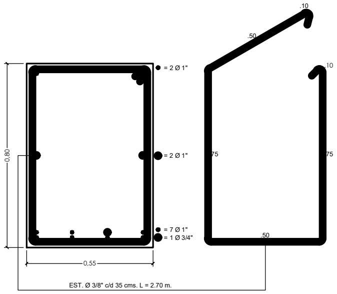
= 2 Ø 1"
= 2 Ø 1"
= 7 Ø 1"
= 1 Ø 3/4"
0,80
0,55
.50
.10
.75
EST. Ø 3/8" c/d 35 cms. L = 2.70 m.

CORTE 41-41' ESC. 1:10

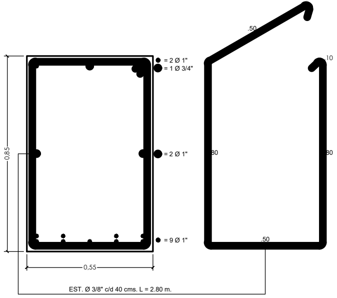
= 2 Ø 1"
= 1 Ø 3/4"
= 2 Ø 1"
= 9 Ø 1"
0,85
0,55
.50
.10
.80
EST. Ø 3/8" c/d 40 cms. L = 2.80 m.

CORTE 42-42' ESC. 1:10

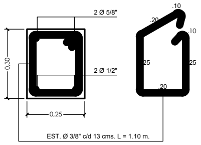
2 Ø 5/8"
2 Ø 1/2"
0,30
0,25
.20
.10
.25
EST. Ø 3/8" c/d 13 cms. L = 1.10 m.

CORTE 43-43' ESC. 1:10

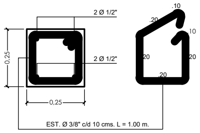
2 Ø 1/2"
2 Ø 1/2"
0,25
0,25
.20
.10
EST. Ø 3/8" c/d 10 cms. L = 1.00 m.

CORTE 44-44' ESC. 1:10

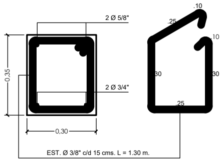
2 Ø 5/8"
2 Ø 3/4"
0,35
0,30
.25
.10
.30
EST. Ø 3/8" c/d 15 cms. L = 1.30 m.

CORTE 45-45' ESC. 1:10

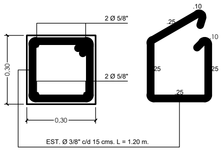
2 Ø 5/8"
2 Ø 5/8"
0,30
0,30
.25
.10
EST. Ø 3/8" c/d 15 cms. L = 1.20 m.

CORTE 46-46' ESC. 1:10

PÓRTICO 1 NIVEL 1 = PORTICO 1 NIVEL 2 (45 X 60) (1° Y 2° PISO)

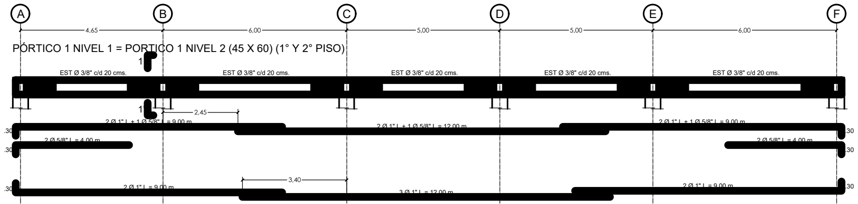
A
B
C
D
E
F
4,65
6,00
5,00
5,00
6,00
1
EST Ø 3/8" c/d 20 cms.
EST Ø 3/8" c/d 20 cms.
EST Ø 3/8" c/d 20 cms.
EST Ø 3/8" c/d 20 cms.
EST Ø 3/8" c/d 20 cms.
1'
2,45
2 Ø 1" L + 1 Ø 5/8" L = 9.00 m
2 Ø 1" L + 1 Ø 5/8" L = 12.00 m
2 Ø 1" L + 1 Ø 5/8" L = 9.00 m
2 Ø 5/8" L = 4.00 m
2 Ø 5/8" L = 4.00 m
3,40
2 Ø 1" L = 9.00 m
3 Ø 1" L = 12.00 m
2 Ø 1" L = 9.00 m
.30

Portico 1 Esc. 1: 75

Gregorio H. Garzón Jaimes
PROPIETARIO
C.I. 9.218.667

Luz Marina Casanova J.
ARQUITECTO
C.I. 9.233.680 C.I.V. 95.596

Gersón Vivas Roa
INGENIERO
C.I. 9.207.969 C.I.V. 71.525

No. de Hoja:

SERIE:

E-16/36

PROYECTO. SUPERMERCADO EXPRESS Y OFICINAS CORPORATIVAS

PROPIETARIO: GARZÓN HIPERMERCADO C.A.

UBICACION: AV. PUEBLO NUEVO. MUNICIPIO SAN CRISTOBAL. EDO. TACHIRA.

CONTENIDO: ESTRUCTURA
VIGAS ESPECIALES Y EN VOLADO

ARQUITECTO: LUZ MARINA CASANOVA. C.I.V. 95.596

N° CATASTRAL: 20-23-04-U01-010-007-011-000-P00-000

DIBUJO: OTTO

FECHA: MARZO 2011

ESCALA: 1/75