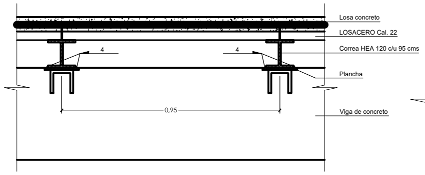

FIJACION LOSACERO

ESC. 1:10

Espesor = 10 cms

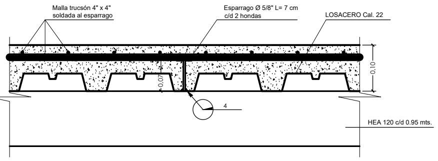

DETALLE LOSACERO ENTREPISO

ESC. 1:5

Espesor = 10 cms

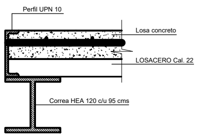

REMATE LATERAL

ESC. 1:5

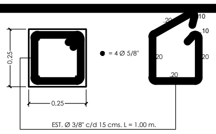

DETALLE COLUMNA 19 (C19)

ESC. 1:10

LOSACERO PLANTA BAJA, 1°, 2° y 3° PISO

Espesor = 10 cm, con esparrago Ø 5/8" L = 7 cm.

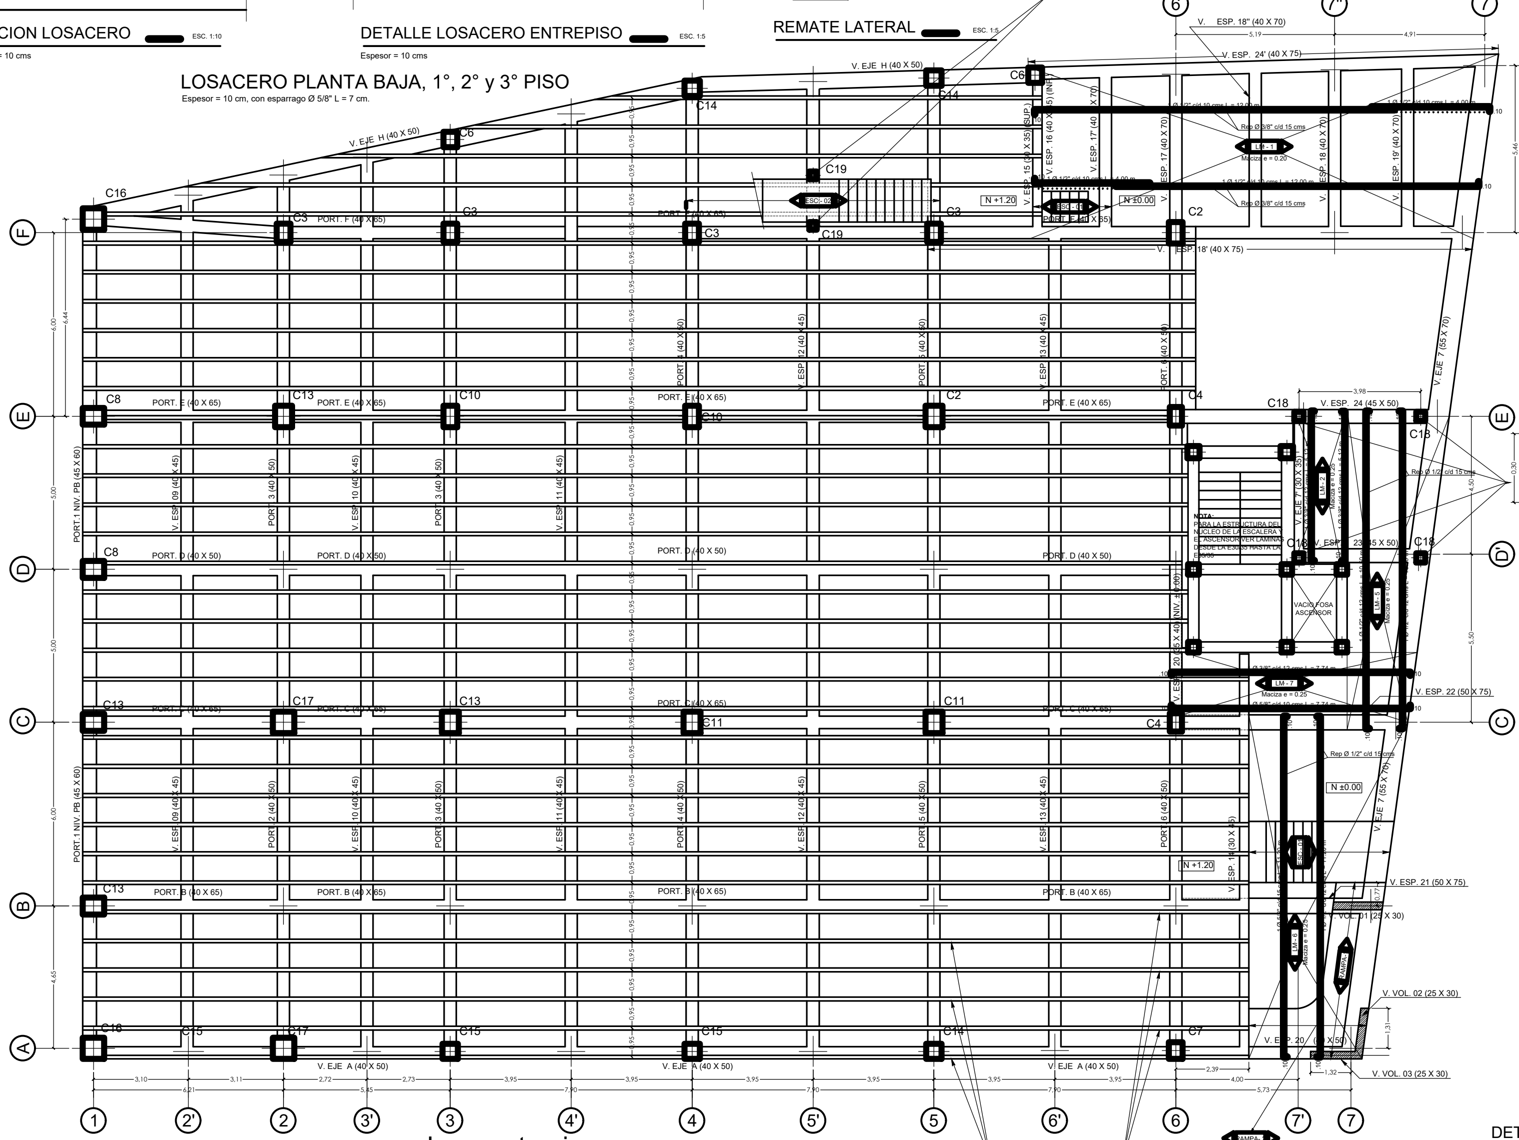

Losa entrepiso Loseta e = 10 cms.

Esc. 1: 75

NIVEL (+1,20) (PLANTA BAJA) (PB)

CORREAS HEA120 c /u 0.95m

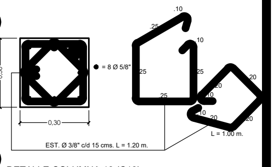

DETALLE COLUMNA 18 (C18)

ESC. 1:10

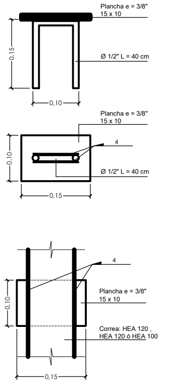

DETALLE PLANCHA

ESC. 1:5

Gregorio H. Garzón Jaimes
PROPIETARIO
C.I. 9.218.667

Luz Marina Casanova J.
ARQUITECTO
C.I. 9.233.680 C.I.V. 95.596

Gersón Vivas Roa
INGENIERO
C.I. 9.207.969 C.I.V. 71.525

No. de Hoja:

SERIE:

E-7/36

PROYECTO. SUPERMERCADO EXPRESS
Y OFICINAS CORPORATIVAS

PROPIETARIO: GARZÓN HIPERMERCADO C.A.
UBICACION: AV. PUEBLO NUEVO.
MUNICIPIO SAN CRISTOBAL. EDO. TACHIRA.
ARQUITECTO: LUZ MARINA CASANOVA. C.I.V. 95.596
DIBUJO: OTTO
CONTENIDO: ESTRUCTURA
ENTREISO P. BAJA (NIVEL +1.20)
N° CATASTRAL: 20-23-04-U01-010-007-011-000-P00-000
FECHA: MARZO 2011
ESCALA: 1/75

Garzón