V. ESP 11 (PB) (40 X 45) (PLANTA BAJA)

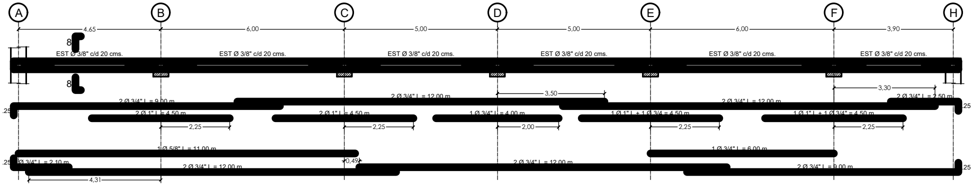
A
B
C
D
E
F
H
4,65
6,00
5,00
5,00
6,00
3,90
8
8'
EST Ø 3/8" c/d 20 cms.
2 Ø 3/4" L = 9.00 m
2 Ø 3/4" L = 12.00 m
3,50
3,30
2 Ø 3/4" L = 12.00 m
2 Ø 3/4" L = 2.50 m
2 Ø 1" L = 4.50 m
2 Ø 1" L = 4.50 m
1 Ø 3/4" L = 4.00 m
1 Ø 1" + 1 Ø 3/4 = 4.50 m
1 Ø 1" + 1 Ø 3/4" = 4.50 m
2,25
2,00
1 Ø 5/8" L = 11.00 m
1 Ø 3/4" L = 6.00 m
2 Ø 3/4" L = 2.10 m
2 Ø 3/4" L = 12.00 m
0,49
2 Ø 3/4" L = 12.00 m
2 Ø 3/4" L = 9.00 m
4,31
.25

V. ESP 13 (PB) (40 X 45) (PLANTA BAJA)

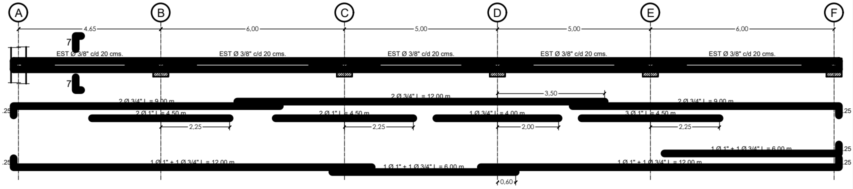
A
B
C
D
E
F
4,65
6,00
5,00
5,00
6,00
7
7'
EST Ø 3/8" c/d 20 cms.
2 Ø 3/4" L = 9.00 m
2 Ø 3/4" L = 12.00 m
3,50
2 Ø 3/4" L = 9.00 m
2 Ø 1" L = 4.50 m
2 Ø 1" L = 4.50 m
1 Ø 3/4" L = 4.00 m
3 Ø 1" L = 4.50 m
2,25
2,00
1 Ø 1" + 1 Ø 3/4" L = 6.00 m
1 Ø 1" + 1 Ø 3/4" L = 12.00 m
1 Ø 1" + 1 Ø 3/4" L = 6.00 m
1 Ø 1" + 1 Ø 3/4" L = 12.00 m
0,60
.25

V. ESP 14 (PB) (30 X 45) (PLANTA BAJA)

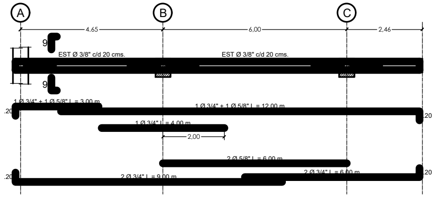
A
B
C
4,65
6,00
2,46
9
9'
EST Ø 3/8" c/d 20 cms.
1 Ø 3/4" + 1 Ø 5/8" L = 3.00 m
1 Ø 3/4" + 1 Ø 5/8" L = 12.00 m
1 Ø 3/4" L = 4.00 m
2,00
2 Ø 5/8" L = 6.00 m
2 Ø 3/4" L = 6.00 m
2 Ø 3/4" L = 9.00 m
.20

V. ESP 15 (PB) (30 X 35) (PTA BAJA)
NIVEL + 1.20

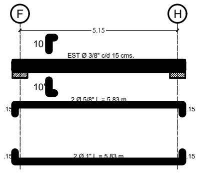
F
H
5,15
10
10'
EST Ø 3/8" c/d 15 cms.
2 Ø 5/8" L = 5.83 m
2 Ø 1" L = 5.83 m
.15

V. ESP 12 (PB) (40 X 45) (PLANTA BAJA)

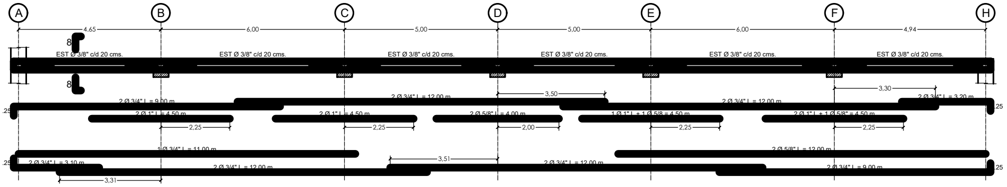
A
B
C
D
E
F
H
4,65
6,00
5,00
5,00
6,00
4,94
8
8'
EST Ø 3/8" c/d 20 cms.
2 Ø 3/4" L = 9.00 m
2 Ø 3/4" L = 12.00 m
3,50
3,30
2 Ø 3/4" L = 12.00 m
2 Ø 3/4" L = 3.20 m
2 Ø 1" L = 4.50 m
2 Ø 1" L = 4.50 m
2 Ø 5/8" L = 4.00 m
1 Ø 1" + 1 Ø 5/8 = 4.50 m
2 Ø 1" L + 1 Ø 5/8" = 4.50 m
2,25
2,00
1 Ø 3/4" L = 11.00 m
2 Ø 5/8" L = 12.00 m
2 Ø 3/4" L = 3.10 m
3,51
2 Ø 3/4" L = 12.00 m
2 Ø 3/4" L = 12.00 m
2 Ø 3/4" L = 9.00 m
3,31
.25

V. ESP 18' (PB) (40 X 75) (PLANTA BAJA) NIVEL ± 0.00

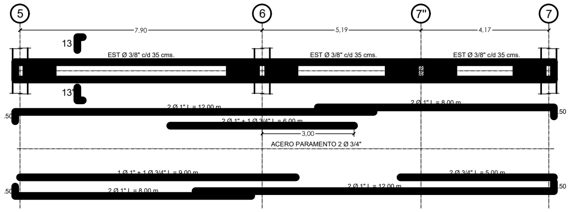
5
6
7''
7
7.90
5,19
4,17
13
13'
EST Ø 3/8" c/d 35 cms.
2 Ø 1" L = 12.00 m
2 Ø 1" L = 8.00 m
2 Ø 1" + 1 Ø 3/4" L = 6.00 m
3,00
ACERO PARAMENTO 2 Ø 3/4"
1 Ø 1" + 1 Ø 3/4" L = 9.00 m
2 Ø 3/4" L = 5.00 m
2 Ø 1" L = 8.00 m
2 Ø 1" L = 12.00 m
.50

V. ESP 18'' (PB) (40 X 70) (PLANTA BAJA)
NIVEL ± 0.00

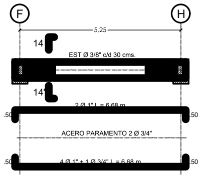
F
H
5,25
14
14'
EST Ø 3/8" c/d 30 cms.
2 Ø 1" L = 6.68 m
ACERO PARAMENTO 2 Ø 3/4"
4 Ø 1" + 1 Ø 3/4" L = 6.68 m
.50

V. ESP 16 (PB) (40 X 45) (PLANTA BAJA)
NIVEL ± 0.00

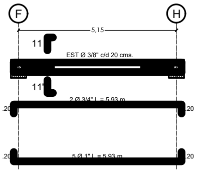
F
H
5,15
11
11'
EST Ø 3/8" c/d 20 cms.
2 Ø 3/4" L = 5.93 m
5 Ø 1" L = 5.93 m
.20

V. ESP 17 (PB) (40 X 70) (PLANTA BAJA)
NIVEL ± 0.00

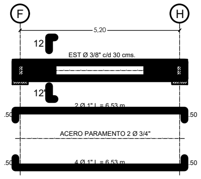
F
H
5,20
12
12'
EST Ø 3/8" c/d 30 cms.
2 Ø 1" L = 6.53 m
ACERO PARAMENTO 2 Ø 3/4"
4 Ø 1" L = 6.53 m
.50

V. ESP 17' (PB) (40 X 70) (PLANTA BAJA)
NIVEL ± 0.00

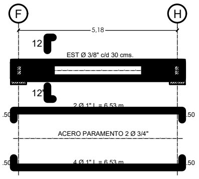
F
H
5,18
12
12'
EST Ø 3/8" c/d 30 cms.
2 Ø 1" L = 6.53 m
ACERO PARAMENTO 2 Ø 3/4"
4 Ø 1" L = 6.53 m
.50

V. ESP 18 (PB) (40 X 70) (PLANTA BAJA)
NIVEL ± 0.00

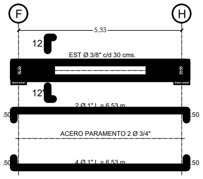
F
H
5,33
12
12'
EST Ø 3/8" c/d 30 cms.
2 Ø 1" L = 6.53 m
ACERO PARAMENTO 2 Ø 3/4"
4 Ø 1" L = 6.53 m
.50

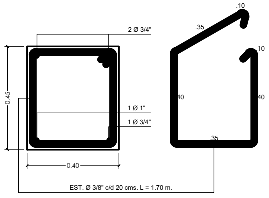
2 Ø 3/4"
1 Ø 1"
1 Ø 3/4"
0,45
0,40
.35
.10
.40
EST. Ø 3/8" c/d 20 cms. L = 1.70 m.

CORTE 7-7' ESC. 1:10

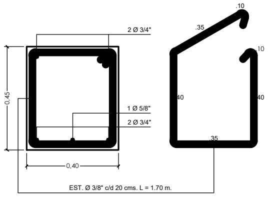
2 Ø 3/4"
1 Ø 5/8"
2 Ø 3/4"
0,45
0,40
.35
.10
.40
EST. Ø 3/8" c/d 20 cms. L = 1.70 m.

CORTE 8-8' ESC. 1:10

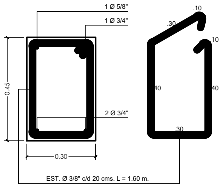
1 Ø 5/8"
1 Ø 3/4"
2 Ø 3/4"
0,45
0,30
.30
.10
.40
EST. Ø 3/8" c/d 20 cms. L = 1.60 m.

CORTE 9-9' ESC. 1:10

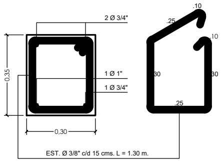
2 Ø 3/4"
1 Ø 1"
1 Ø 3/4"
0,35
0,30
.25
.10
.30
EST. Ø 3/8" c/d 15 cms. L = 1.30 m.

CORTE 10-10' ESC. 1:10

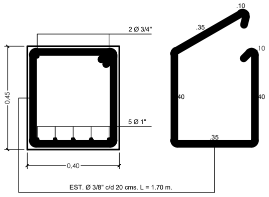
2 Ø 3/4"
5 Ø 1"
0,45
0,40
.35
.10
.40
EST. Ø 3/8" c/d 20 cms. L = 1.70 m.

CORTE 11-11' ESC. 1:10

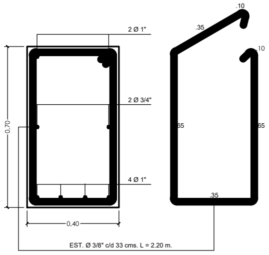
2 Ø 1"
2 Ø 3/4"
4 Ø 1"
0,70
0,40
.35
.10
.65
EST. Ø 3/8" c/d 33 cms. L = 2.20 m.

CORTE 12-12' ESC. 1:10

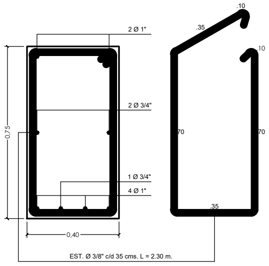
2 Ø 1"
2 Ø 3/4"
1 Ø 3/4"
4 Ø 1"
0,75
0,40
.35
.10
.70
EST. Ø 3/8" c/d 35 cms. L = 2.30 m.

CORTE 13-13' ESC. 1:10

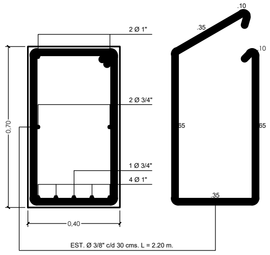
2 Ø 1"
2 Ø 3/4"
1 Ø 3/4"
4 Ø 1"
0,70
0,40
.35
.10
.65
EST. Ø 3/8" c/d 30 cms. L = 2.20 m.

CORTE 14-14' ESC. 1:10

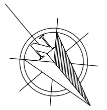

Gregorio H. Garzón Jaimes
PROPIETARIO
C.I. 9.218.667

Luz Marina Casanova J.
ARQUITECTO
C.I. 9.233.680 C.I.V. 95.596

Gersón Vivas Roa
INGENIERO
C.I. 9.207.969 C.I.V. 71.525

No. de Hoja:

SERIE:

E-13/36

PROYECTO. SUPERMERCADO EXPRESS
Y OFICINAS CORPORATIVAS

PROPIETARIO: GARZÓN HIPERMERCADO C.A.
UBICACION: AV. PUEBLO NUEVO. MUNICIPIO SAN CRISTOBAL. EDO. TACHIRA.
CONTENIDO: ESTRUCTURA VIGAS ESPECIALES
ARQUITECTO: LUZ MARINA CASANOVA. C.I.V. 95.596
N° CATASTRAL: 20-23-04-U01-010-007-011-000-P00-000
DIBUJO: OTTO
FECHA: MARZO 2011
ESCALA: 1/75