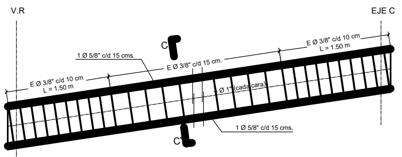

LM - 8 = LM - 9 Esc. 1:20

Esp. = 40 cms.

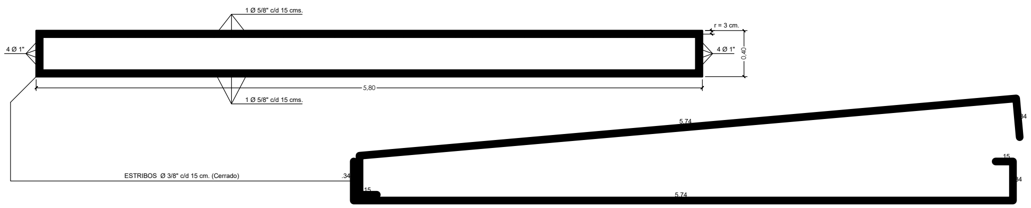

Corte C-C' Esc. 1:20

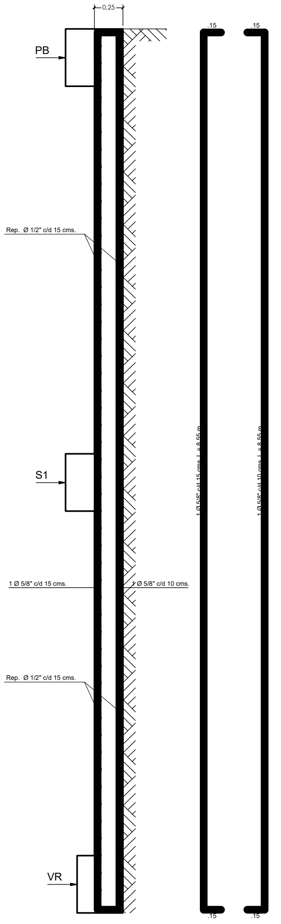

Pantalla ejes A - H Esc. 1:20

Maciza e = 25 cms

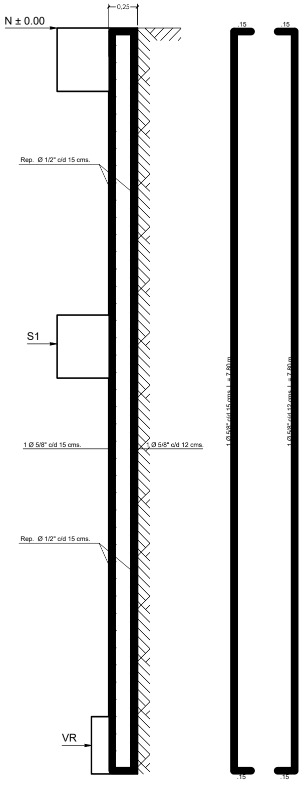

Pantalla eje 7 Esc. 1:20

Maciza e = 25 cms

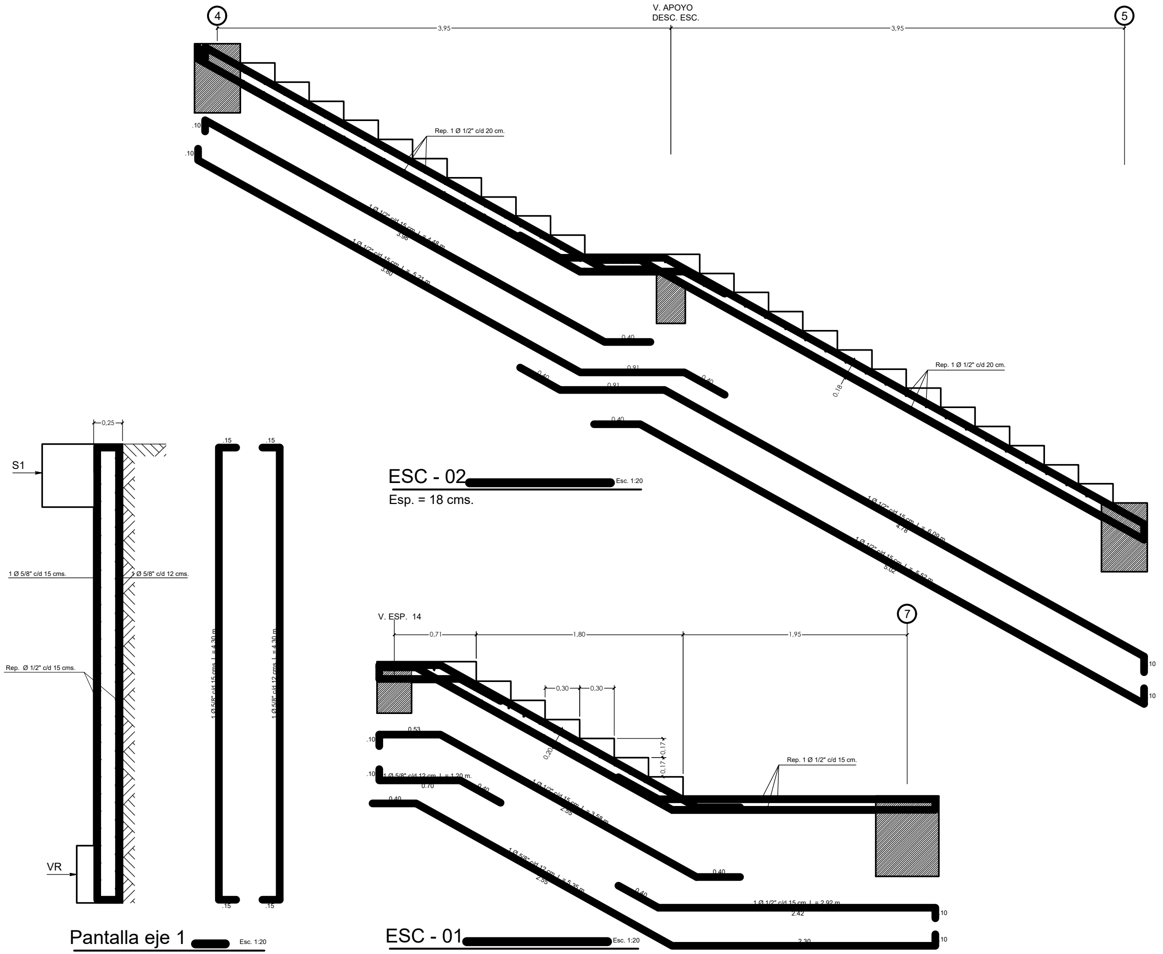

Pantalla eje 1 Esc. 1:20

Maciza e = 25 cms

ESC - 02 Esc. 1:20

Esp. = 18 cms.

ESC - 01 Esc. 1:20

Esp. = 20 cms.

Gregorio H. Garzón Jaimes
PROPIETARIO
C.I. 9.218.667

Luz Marina Casanova J.
ARQUITECTO
C.I. 9.233.680 C.I.V. 95.596

Gersón Vivas Roa
INGENIERO
C.I. 9.207.969 C.I.V. 71.525

No. de Hoja:

SERIE:

E-4/36

PROYECTO. SUPERMERCADO EXPRESS
Y OFICINAS CORPORATIVAS

PROPIETARIO: GARZÓN HIPERMERCADO C.A.

UBICACION: AV. PUEBLO NUEVO.
MUNICIPIO SAN CRISTOBAL. EDO. TACHIRA.

CONTENIDO: ESTRUCTURA
PANTALLAS, RAMPA Y ESCALERA

ARQUITECTO: LUZ MARINA CASANOVA. C.I.V. 95.596

N° CATASTRAL: 20-23-04-U01-010-007-011-000-P00-000

DIBUJO: OTTO

FECHA: MARZO 2011

ESCALA: 1/20