V. ESP 20 (PB) (40 X 50) (PLANTA BAJA)
NIVEL ± 0.00

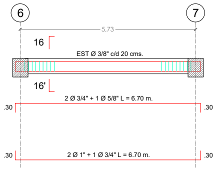
6
7
5,73
16
16'
EST Ø 3/8" c/d 20 cms.
2 Ø 3/4" + 1 Ø 5/8" L = 6.70 m.
.30
2 Ø 1" + 1 Ø 3/4" L = 6.70 m.
.30

V. ESP 20' (PB) (35 X 40) (PTA. BAJA)
NIVEL ± 0.00

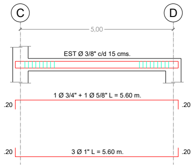

V. ESP 21 (PB) (50 X 75) (PLANTA BAJA)
NIVEL ± 0.00

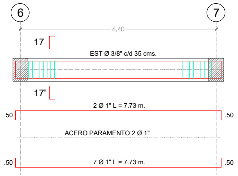

V. ESP 22 (PB) (50 X 75) (PLANTA BAJA)
NIVEL ± 0.00

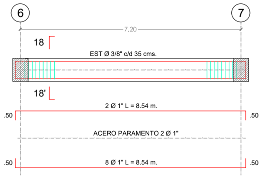

V. ESP 23 (PB) (45 X 50)
(PLANTA BAJA) NIVEL ± 0.00

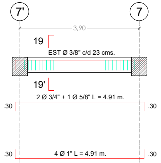

V. ESP 24 (PB) (45 X 50)
(PLANTA BAJA) NIVEL ± 0.00

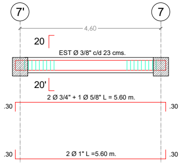

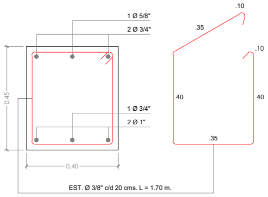

CORTE 16-16' ESC. 1:10

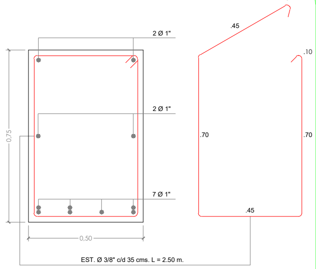

CORTE 17-17' ESC. 1:10

V. ESP 25 (N1) (30 X 40) (1° PISO)

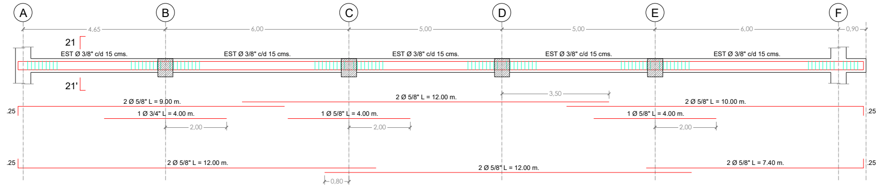

V. ESP 26 (N1) (40 X 70) (1° PISO)

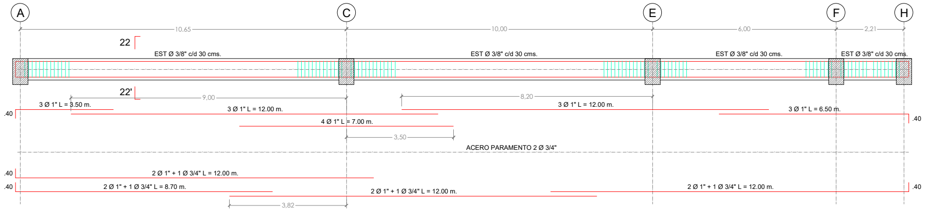

V. ESP 27 (N1) (40 X 70) (1° PISO)

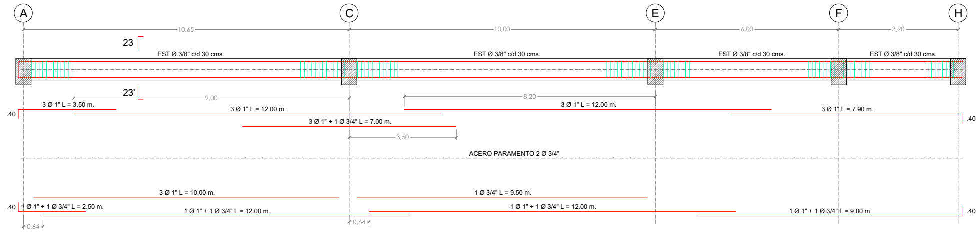

V. ESP 28 = V. ESP. 29 (N1) (40 X 65) (1° PISO)

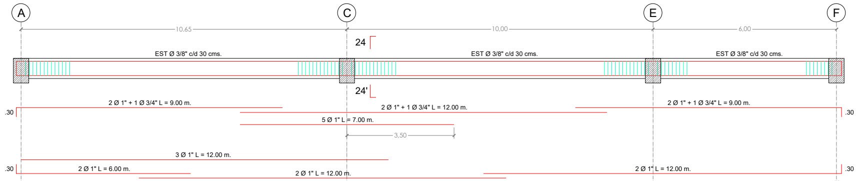

V. ESP 30 (N1) (25 X 35)
(1° PISO)

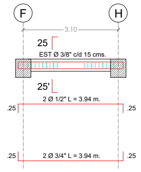

V. ESP 31 (N1) (30 X 45) (1° PISO)

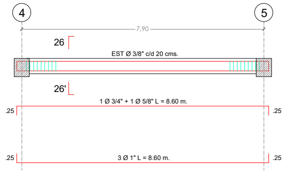

V. ESP 32 (N1) (30 X 35) (1° PISO)

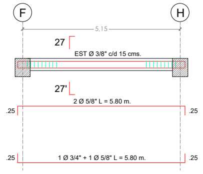

V. ESP 32' (N1) (25 X 35) (1° PISO)

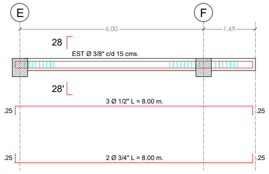

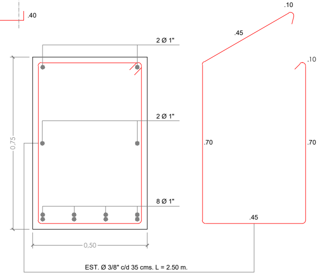

CORTE 18-18' ESC. 1:10

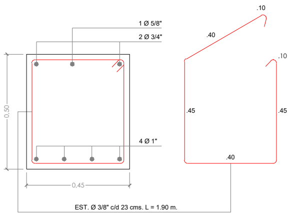

CORTE 19-19' ESC. 1:10

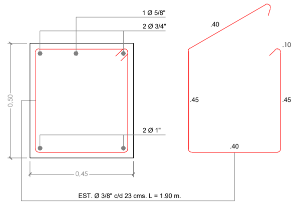

CORTE 20-20' ESC. 1:10

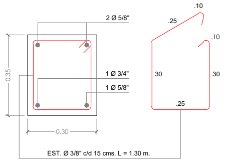

CORTE 27-27' ESC. 1:10

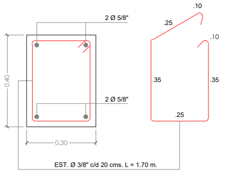

CORTE 21-21' ESC. 1:10

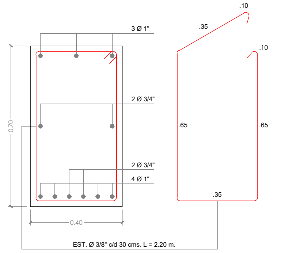

CORTE 22-22' ESC. 1:10

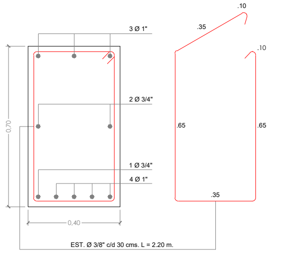

CORTE 23-23' ESC. 1:10

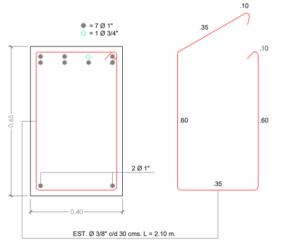

CORTE 24-24' ESC. 1:10

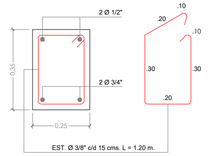

CORTE 25-25' ESC. 1:10

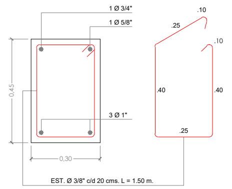

CORTE 26-26' ESC. 1:10

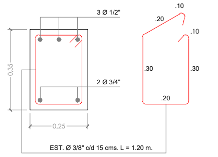

CORTE 28-28' ESC. 1:10

Gregorio H. Garzón Jaimes
PROPIETARIO
C.I. 9.218.667

Luz Marina Casanova J.
ARQUITECTO
C.I. 9.233.680 C.I.V. 95.596

Gersón Vivas Roa
INGENIERO
C.I. 9.207.969 C.I.V. 71.525

No. de Hoja:

SERIE:

E-14/36

PROYECTO. SUPERMERCADO EXPRESS Y OFICINAS CORPORATIVAS.

PROPIETARIO: GARZÓN HIPERMERCADO C.A.

UBICACION: AV. PUEBLO NUEVO. MUNICIPIO SAN CRISTOBAL. EDO. TACHIRA.

CONTENIDO: ESTRUCTURA VIGAS ESPECIALES

ARQUITECTO: LUZ MARINA CASANOVA. C.I.V. 95.596

N° CATASTRAL: 20-23-04-U01-010-007-011-000-P00-000

DIBUJO: OTTO

FECHA: MARZO 2011

ESCALA: 1/75