V. AMARRE (N1 Y N2) (30 X 30) (1° Y 2 ° PISO)

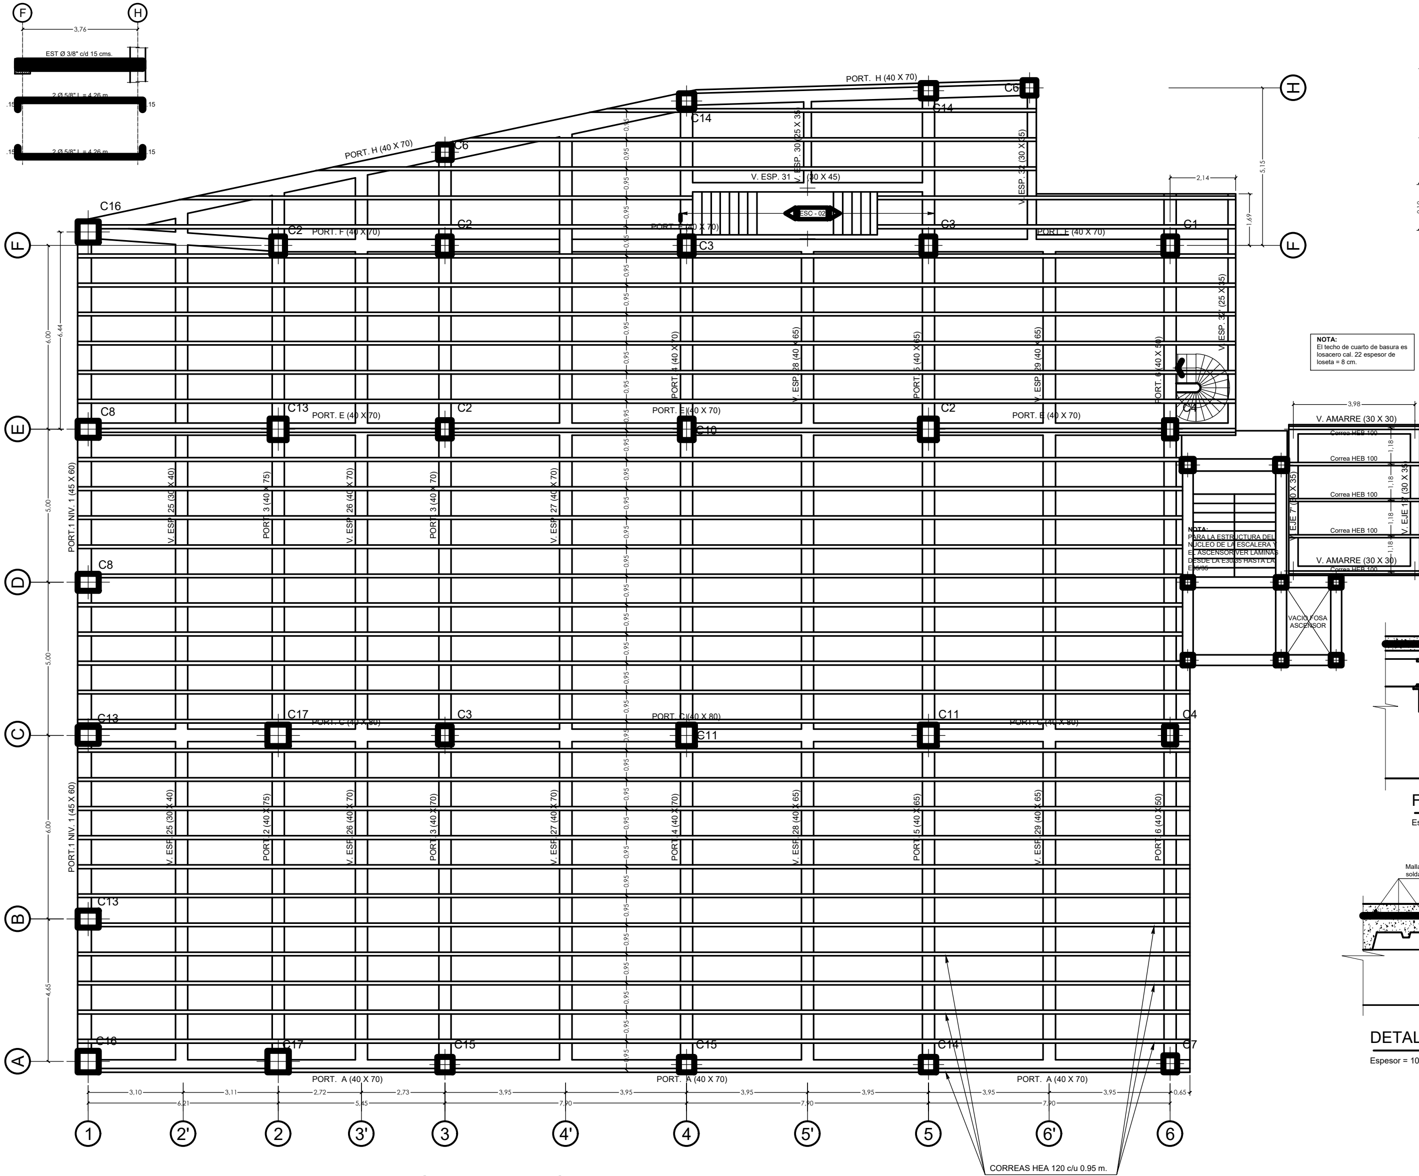

NOTA:
El techo de cuarto de basura es losacero cal. 22 espesor de loseta = 8 cm.

NOTA:
Ver despieces de la V. EJE 7', la V. EJE 19 y la V. AMARRE en la lámina E-9/35

Losa entrepiso Loseta e = 10 cms. Esc. 1: 75

NIVEL (+5,20) (1° PISO) (N1)

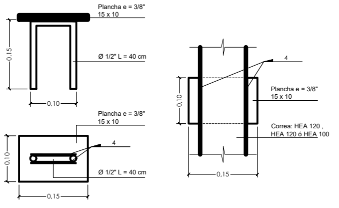

DETALLE PLANCHA ESC. 1:5

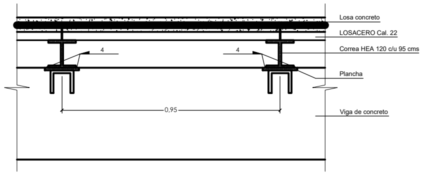

FIJACION LOSACERO ESC. 1:10

Espesor = 10 cms

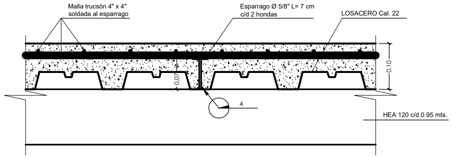

DETALLE LOSACERO ENTREPISO ESC. 1:5

Espesor = 10 cms

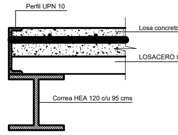

REMATE LATERAL ESC. 1:5

LOSACERO PLANTA BAJA, 1°, 2° y 3° PISO

Espesor = 10 cm, con esparrago Ø 5/8" L = 7 cm.

Gregorio H. Garzón Jaimes
PROPIETARIO
C.I. 9.218.667

Luz Marina Casanova J.
ARQUITECTO
C.I. 9.233.680 C.I.V. 95.596

Gersón Vivas Roa
INGENIERO
C.I. 9.207.969 C.I.V. 71.525

No. de Hoja:
SERIE:
E-8/36

PROYECTO. SUPERMERCADO EXPRESS
Y OFICINAS CORPORATIVAS

PROPIETARIO: GARZÓN HIPERMERCADO C.A.
UBICACION: AV. PUEBLO NUEVO. MUNICIPIO SAN CRISTOBAL. EDO. TACHIRA.
ARQUITECTO: LUZ MARINA CASANOVA. C.I.V. 95.596
DIBUJO: OTTO
CONTENIDO: ESTRUCTURA
ENTREPISO 1° PISO (NIVEL +5.20 (N1
N° CATASTRAL: 20-23-04-U01-010-007-011-000-P00-000
FECHA: MARZO 2011
ESCALA: 1/75

Garzón