V. AMARRE (N1 Y N2) (30 X 30) (1° Y 2 ° PISO)

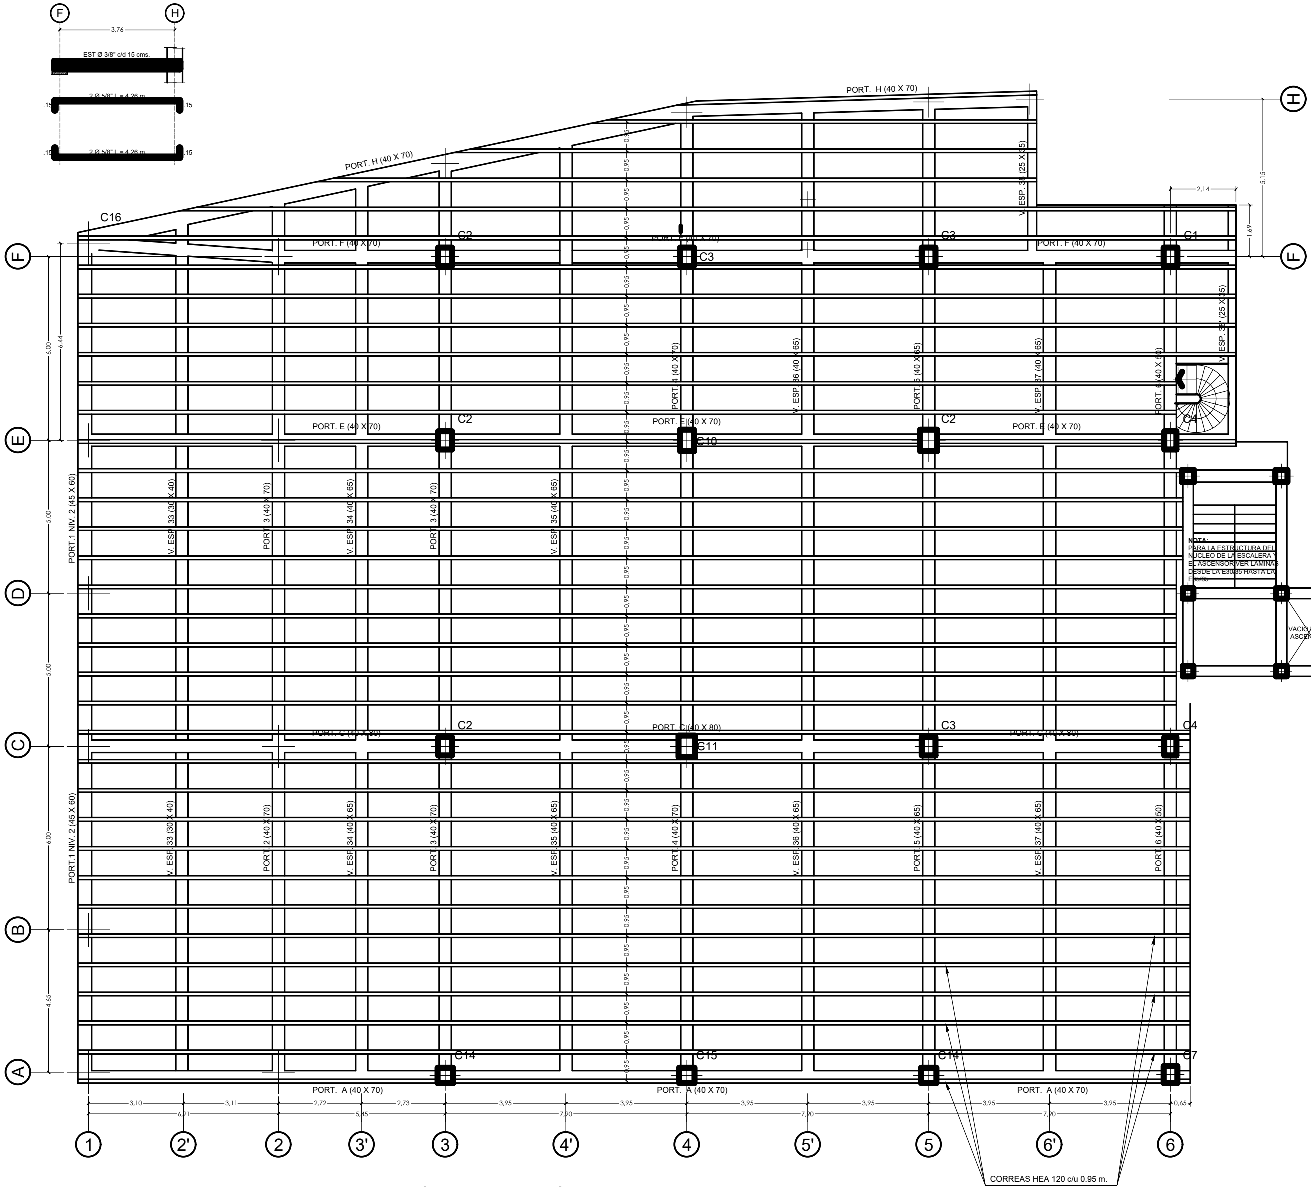

NOTA:
PARA LA ESTRUCTURA DEL NUCLEO DE LA ESCALERA Y EL ASCENSOR VER LAMINAS DESDE LA E30/35 HASTA LA E35/35

Losa entrepiso Loseta e = 10 cms.

Esc. 1: 75

NIVEL (+8.80) (2° PISO) (N2)

CORREAS HEA 120 c /u 0.95m

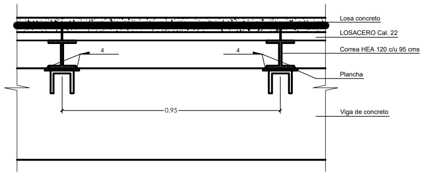

FIJACION LOSACERO

ESC. 1:10

Espesor = 10 cms

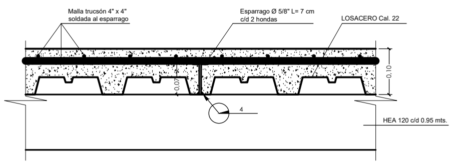

DETALLE LOSACERO ENTREPISO

ESC. 1:5

Espesor = 10 cms

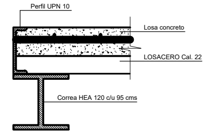

REMATE LATERAL

ESC. 1:5

LOSACERO PLANTA BAJA, 1°, 2° y 3° PISO

Espesor = 10 cm, con esparrago Ø 5/8" L = 7 cm.

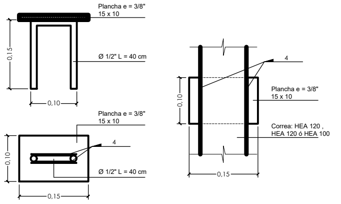

DETALLE PLANCHA

ESC. 1:5

Gregorio H. Garzón Jaimes
PROPIETARIO
C.I. 9.218.667

Luz Marina Casanova J.
ARQUITECTO
C.I. 9.233.680 C.I.V. 95.596

Gersón Vivas Roa
INGENIERO
C.I. 9.207.969 C.I.V. 71.525

No. de Hoja:

SERIE:

E-9/36

PROYECTO: SUPERMERCADO EXPRESS
Y OFICINAS CORPORATIVAS

PROPIETARIO: GARZÓN HIPERMERCADO C.A.

UBICACION: AV. PUEBLO NUEVO.
MUNICIPIO SAN CRISTOBAL. EDO. TACHIRA.

CONTENIDO: ESTRUCTURA
ENTREPISO 2° PISO (NIVEL +8.40 (N2

ARQUITECTO: LUZ MARINA CASANOVA. C.I.V. 95.596

N° CATASTRAL: 20-23-04-U01-010-007-011-000-P00-000

DIBUJO: OTTO

FECHA: MARZO 2011

ESCALA: 1/75

Garzón