V. ESP 33 (N2) (30 X 40) (2° PISO)

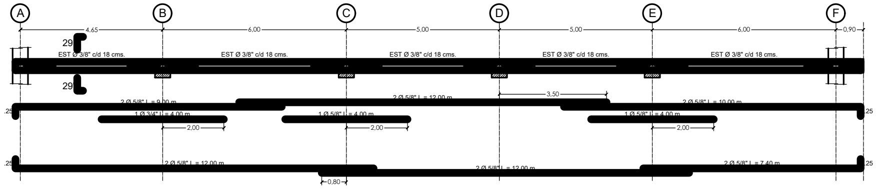
A
B
C
D
E
F
4.65
6,00
5,00
5,00
6,00
0,90
29
29
EST Ø 3/8" c/d 18 cms.
EST Ø 3/8" c/d 18 cms.
EST Ø 3/8" c/d 18 cms.
EST Ø 3/8" c/d 18 cms.
EST Ø 3/8" c/d 18 cms.
2 Ø 5/8" L = 9.00 m
2 Ø 5/8" L = 12.00 m
2 Ø 5/8" L = 10.00 m
3,50
1 Ø 3/4" L = 4.00 m
1 Ø 5/8" L = 4.00 m
1 Ø 5/8" L = 4.00 m
2,00
2,00
2,00
.25
.25
2 Ø 5/8" L = 12.00 m
2 Ø 5/8" L = 12.00 m
2 Ø 5/8" L = 7.40 m
0,80

V. ESP 34 (N2) (40 X 65) (2° PISO)

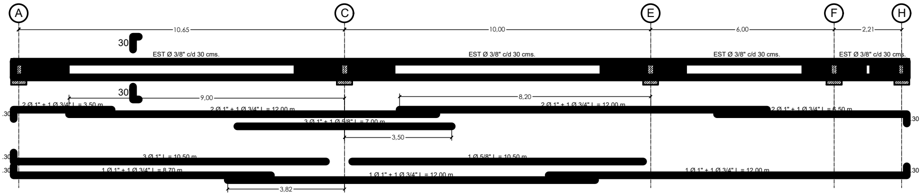
A
C
E
F
H
10.65
10,00
6,00
2,21
30
30
EST Ø 3/8" c/d 30 cms.
EST Ø 3/8" c/d 30 cms.
EST Ø 3/8" c/d 30 cms.
EST Ø 3/8" c/d 30 cms.
9,00
8,20
2 Ø 1" + 1 Ø 3/4" L = 3.50 m
2 Ø 1" + 1 Ø 3/4" L = 12.00 m
2 Ø 1" + 1 Ø 3/4" L = 12.00 m
2 Ø 1" + 1 Ø 3/4" L = 6.50 m
3 Ø 1" + 1 Ø 5/8" L = 7.00 m
3,50
3 Ø 1" L = 10.50 m
1 Ø 5/8" L = 10.50 m
1 Ø 1" + 1 Ø 3/4" L = 8.70 m
1 Ø 1" + 1 Ø 3/4" L = 12.00 m
1 Ø 1" + 1 Ø 3/4" L = 12.00 m
3,82
.30
.30

V. ESP 35 (N2) (40 X 65) (2° PISO)

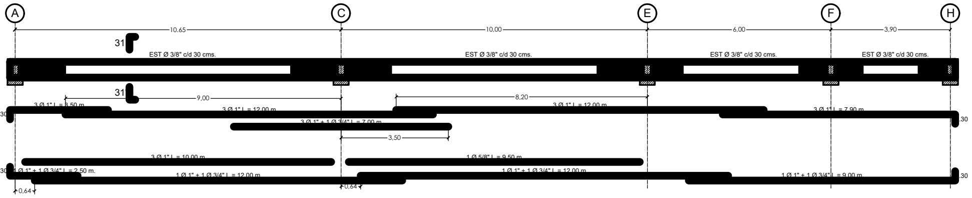
A
C
E
F
H
10.65
10,00
6,00
3,90
31
31
EST Ø 3/8" c/d 30 cms.
EST Ø 3/8" c/d 30 cms.
EST Ø 3/8" c/d 30 cms.
EST Ø 3/8" c/d 30 cms.
9,00
8,20
3 Ø 1" L = 3.50 m
3 Ø 1" L = 12.00 m
3 Ø 1" L = 12.00 m
3 Ø 1" L = 7.90 m
3 Ø 1" + 1 Ø 3/4" L = 7.00 m
3,50
3 Ø 1" L = 10.00 m
1 Ø 5/8" L = 9.50 m
1 Ø 1" + 1 Ø 3/4" L = 2.50 m.
1 Ø 1" + 1 Ø 3/4" L = 12.00 m
1 Ø 1" + 1 Ø 3/4" L = 12.00 m
1 Ø 1" + 1 Ø 3/4" L = 9.00 m
0,64
0,64
.30
.30

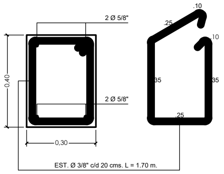
2 Ø 5/8"
2 Ø 5/8"
0,40
0,30
.10
.25
.10
.35
.35
.25
EST. Ø 3/8" c/d 20 cms. L = 1.70 m.

CORTE 29-29' [redacted] ESC. 1:10

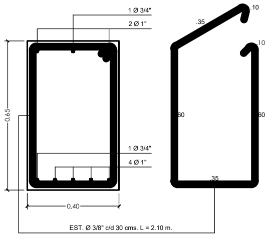
1 Ø 3/4"
2 Ø 1"
1 Ø 3/4"
4 Ø 1"
0,65
0,40
.10
.35
.10
.60
.60
.35
EST. Ø 3/8" c/d 30 cms. L = 2.10 m.

CORTE 30-30' [redacted] ESC. 1:10

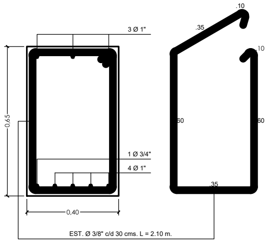
3 Ø 1"
1 Ø 3/4"
4 Ø 1"
0,65
0,40
.10
.35
.10
.60
.60
.35
EST. Ø 3/8" c/d 30 cms. L = 2.10 m.

CORTE 31-31' [redacted] ESC. 1:10

V. ESP 36 (N2) (40 X 65) (2° PISO)

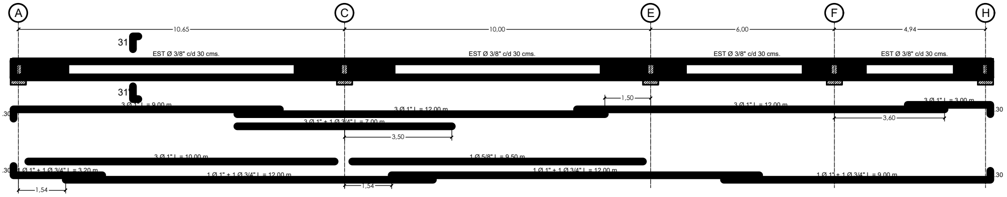
A
C
E
F
H
10.65
10,00
6,00
4,94
31
31
EST Ø 3/8" c/d 30 cms.
EST Ø 3/8" c/d 30 cms.
EST Ø 3/8" c/d 30 cms.
EST Ø 3/8" c/d 30 cms.
1,50
3 Ø 1" L = 9.00 m
3 Ø 1" L = 12.00 m
3 Ø 1" L = 12.00 m
3 Ø 1" L = 3.00 m
3,60
3 Ø 1" + 1 Ø 3/4" L = 7.00 m
3,50
3 Ø 1" L = 10.00 m
1 Ø 5/8" L = 9.50 m
1 Ø 1" + 1 Ø 3/4" L = 3.20 m
1 Ø 1" + 1 Ø 3/4" L = 12.00 m
1 Ø 1" + 1 Ø 3/4" L = 12.00 m
1 Ø 1" + 1 Ø 3/4" L = 9.00 m
1,54
1,54
.30
.30

V. ESP 37 (N2) (40 X 65) (2° PISO)

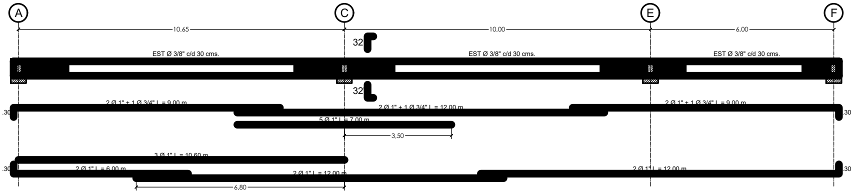
A
C
E
F
10.65
10,00
6,00
32
32
EST Ø 3/8" c/d 30 cms.
EST Ø 3/8" c/d 30 cms.
EST Ø 3/8" c/d 30 cms.
2 Ø 1" + 1 Ø 3/4" L = 9.00 m
2 Ø 1" + 1 Ø 3/4" L = 12.00 m
2 Ø 1" + 1 Ø 3/4" L = 9.00 m
5 Ø 1" L = 7.00 m
3,50
3 Ø 1" L = 10.60 m
2 Ø 1" L = 6.00 m
2 Ø 1" L = 12.00 m
2 Ø 1" L = 12.00 m
6,80
.30
.30

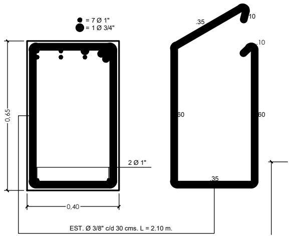
● = 7 Ø 1"
● = 1 Ø 3/4"
2 Ø 1"
0,65
0,40
.10
.35
.10
.60
.60
.35
EST. Ø 3/8" c/d 30 cms. L = 2.10 m.

CORTE 32-32' [redacted] ESC. 1:10

V. ESP 38 (N2) (25 X 35) (2° PISO)

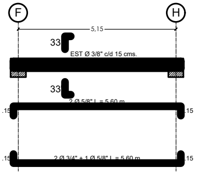
F
H
5,15
33
33
EST Ø 3/8" c/d 15 cms.
2 Ø 5/8" L = 5.60 m
2 Ø 3/4" + 1 Ø 5/8" L = 5.60 m
.15
.15

V. ESP 32' (N1) (25 X 35) (1° PISO)

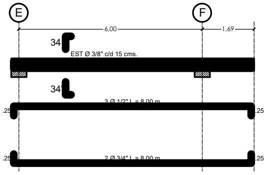
E
F
6,00
1,69
34
34
EST Ø 3/8" c/d 15 cms.
3 Ø 1/2" L = 8.00 m
2 Ø 3/4" L = 8.00 m
.25
.25

V. ESP 39 = V. ESP. 40 (N3) (40 X 70) (3° PISO)

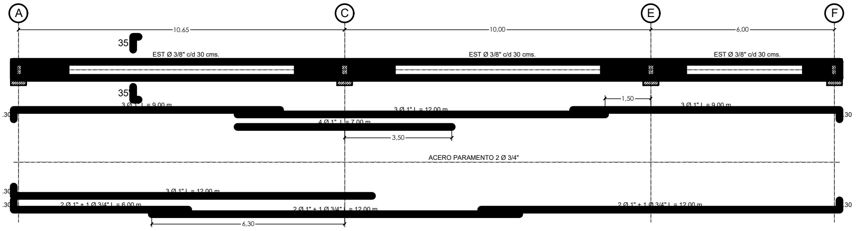
A
C
E
F
10.65
10,00
6,00
35
35
EST Ø 3/8" c/d 30 cms.
EST Ø 3/8" c/d 30 cms.
EST Ø 3/8" c/d 30 cms.
1,50
3 Ø 1" L = 9.00 m
3 Ø 1" L = 12.00 m
3 Ø 1" L = 9.00 m
4 Ø 1" L = 7.00 m
3,50
ACERO PARAMENTO 2 Ø 3/4"
3 Ø 1" L = 12.00 m
2 Ø 1" + 1 Ø 3/4" L = 6.00 m
2 Ø 1" + 1 Ø 3/4" L = 12.00 m
2 Ø 1" + 1 Ø 3/4" L = 12.00 m
6,30
.30
.30

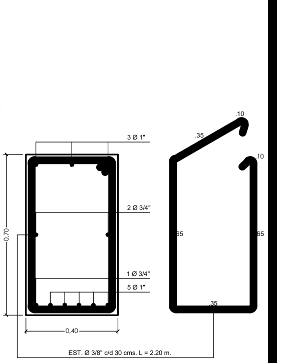
3 Ø 1"
2 Ø 3/4"
1 Ø 3/4"
5 Ø 1"
0,70
0,40
.10
.35
.10
.65
.65
.35
EST. Ø 3/8" c/d 30 cms. L = 2.20 m.

CORTE 35-35' [redacted] ESC. 1:10

V. ESP 39' (N3) (30 X 55) (3° PISO)

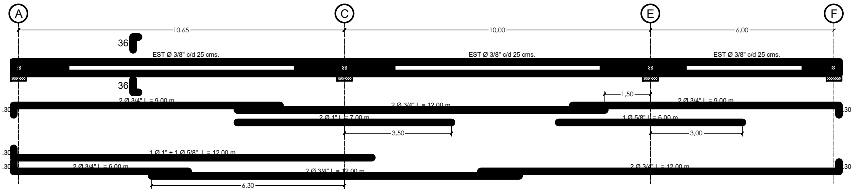
A
C
E
F
10.65
10,00
6,00
36
36
EST Ø 3/8" c/d 25 cms.
EST Ø 3/8" c/d 25 cms.
EST Ø 3/8" c/d 25 cms.
1,50
2 Ø 3/4" L = 9.00 m
2 Ø 3/4" L = 12.00 m
2 Ø 3/4" L = 9.00 m
2 Ø 1" L = 7.00 m
1 Ø 5/8" L = 6.00 m
3,50
3,00
1 Ø 1" + 1 Ø 5/8" L = 12.00 m
2 Ø 3/4" L = 6.00 m
2 Ø 3/4" L = 12.00 m
2 Ø 3/4" L = 12.00 m
6,30
.30
.30

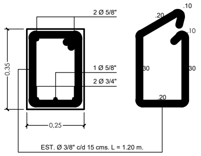
2 Ø 5/8"
1 Ø 5/8"
2 Ø 3/4"
0,35
0,25
.10
.20
.10
.30
.30
.20
EST. Ø 3/8" c/d 15 cms. L = 1.20 m.

CORTE 33-33' [redacted] ESC. 1:10

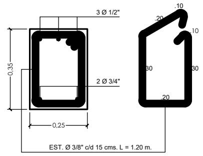
3 Ø 1/2"
2 Ø 3/4"
0,35
0,25
.10
.20
.10
.30
.30
.20
EST. Ø 3/8" c/d 15 cms. L = 1.20 m.

CORTE 34-34' [redacted] ESC. 1:10

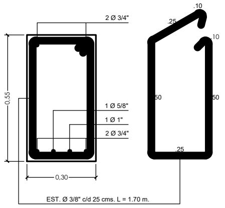
2 Ø 3/4"
1 Ø 5/8"
1 Ø 1"
2 Ø 3/4"
0,55
0,30
.10
.25
.10
.50
.50
.25
EST. Ø 3/8" c/d 25 cms. L = 1.70 m.

CORTE 36-36' [redacted] ESC. 1:10

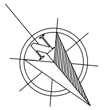

Gregorio H. Garzón Jaimes
PROPIETARIO
C.I. 9.218.667

Luz Marina Casanova J.
ARQUITECTO
C.I. 9.233.680 C.I.V. 95.596

Gersón Vivas Roa
INGENIERO
C.I. 9.207.969 C.I.V. 71.525

PROYECTO. SUPERMERCADO EXPRESS Y OFICINAS CORPORATIVAS

No. de Hoja:

SERIE:

E-15/36

PROPIETARIO: GARZÓN HIPERMERCADO C.A.
UBICACION: AV. PUEBLO NUEVO. MUNICIPIO SAN CRISTOBAL. EDO. TACHIRA.
ARQUITECTO: LUZ MARINA CASANOVA. C.I.V. 95.596
DIBUJO: OTTO
CONTENIDO: ESTRUCTURA VIGAS ESPECIALES
N° CATASTRAL: 20-23-04-U01-010-007-011-000-P00-000
FECHA: MARZO 2011
ESCALA: 1/75

Garzón