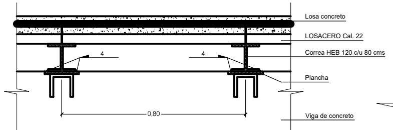

FIJACION LOSACERO
ESC. 1:10

Loseta espesor = 12 cms

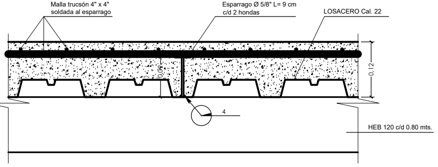

DETALLE LOSACERO ENTREPISO
ESC. 1:5

Loseta espesor = 12 cms

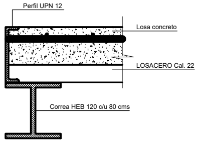

REMATE LATERAL
ESC. 1:5

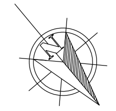

LOSACERO SOTANO 1

Loseta espesor = 12 cm, con esparrago Ø 5/8" L = 9 cm.

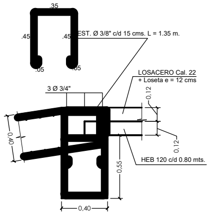

CORTE A-A' ESC. 1:20

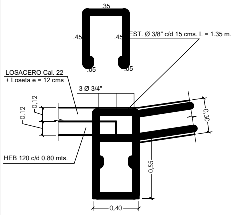

CORTE B-B' ESC. 1:20

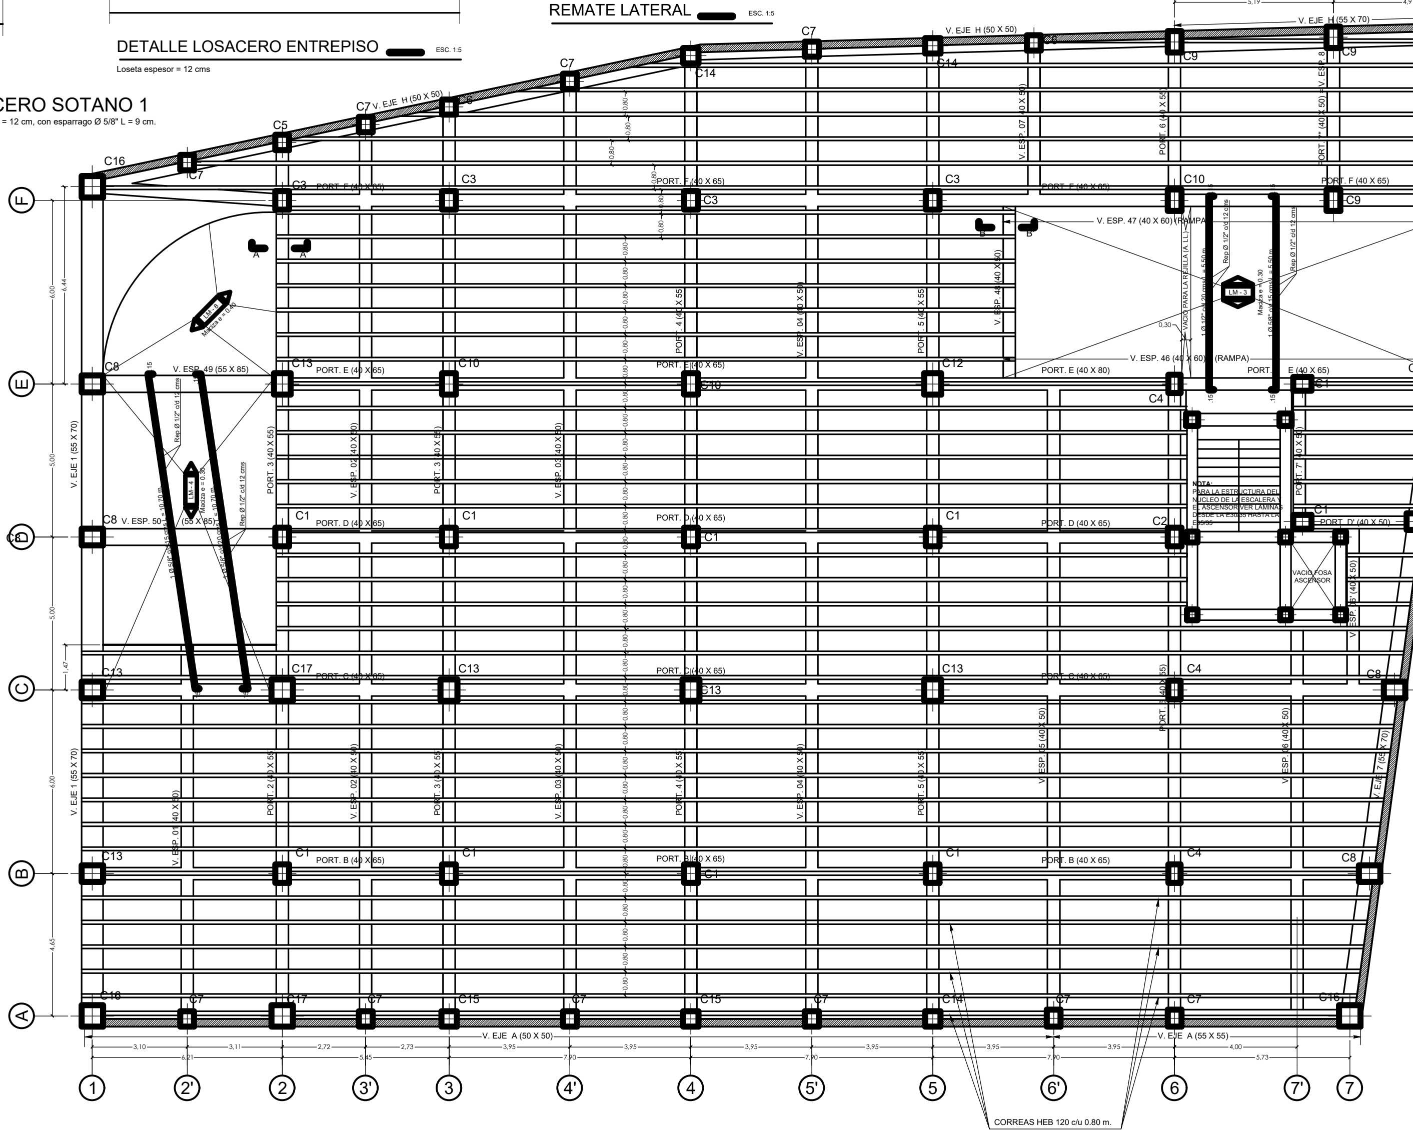

NOTA:
PARA LA ESTRUCTURA DEL NUCLEO DE LA ESCALERA Y EL ASCENSOR VER LAMINAS DESDE LA E30/35 HASTA LA E35/35

Losa entrepiso Loseta e = 12 cms.
Esc. 1: 75

NIVEL (-2,50) (SOTANO 1) (S1)

CORREAS HEB 120 c /u 0.80m

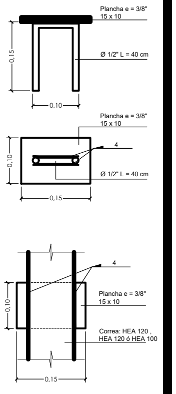

DETALLE PLANCHA
ESC. 1:5

Gregorio H. Garzón Jaimes
PROPIETARIO
C.I. 9.218.667

Luz Marina Casanova J.
ARQUITECTO
C.I. 9.233.680 C.I.V. 95.596

Gersón Vivas Roa
INGENIERO
C.I. 9.207.969 C.I.V. 71.525

No. de Hoja:

SERIE:
E-6/36

PROYECTO. SUPERMERCADO EXPRESS Y OFICINAS CORPORATIVAS

PROPIETARIO: GARZÓN HIPERMERCADO C.A.
UBICACION: AV. PUEBLO NUEVO. MUNICIPIO SAN CRISTOBAL. EDO. TACHIRA.
ARQUITECTO: LUZ MARINA CASANOVA. C.I.V. 95.596
DIBUJO: OTTO
CONTENIDO: ESTRUCTURA ENTREPISO SOT. 1 (S1) (NIVEL -2,50)
N° CATASTRAL: 20-23-04-U01-010-007-011-000-P00-000
FECHA: MARZO 2011
ESCALA: 1/75

Garzón