
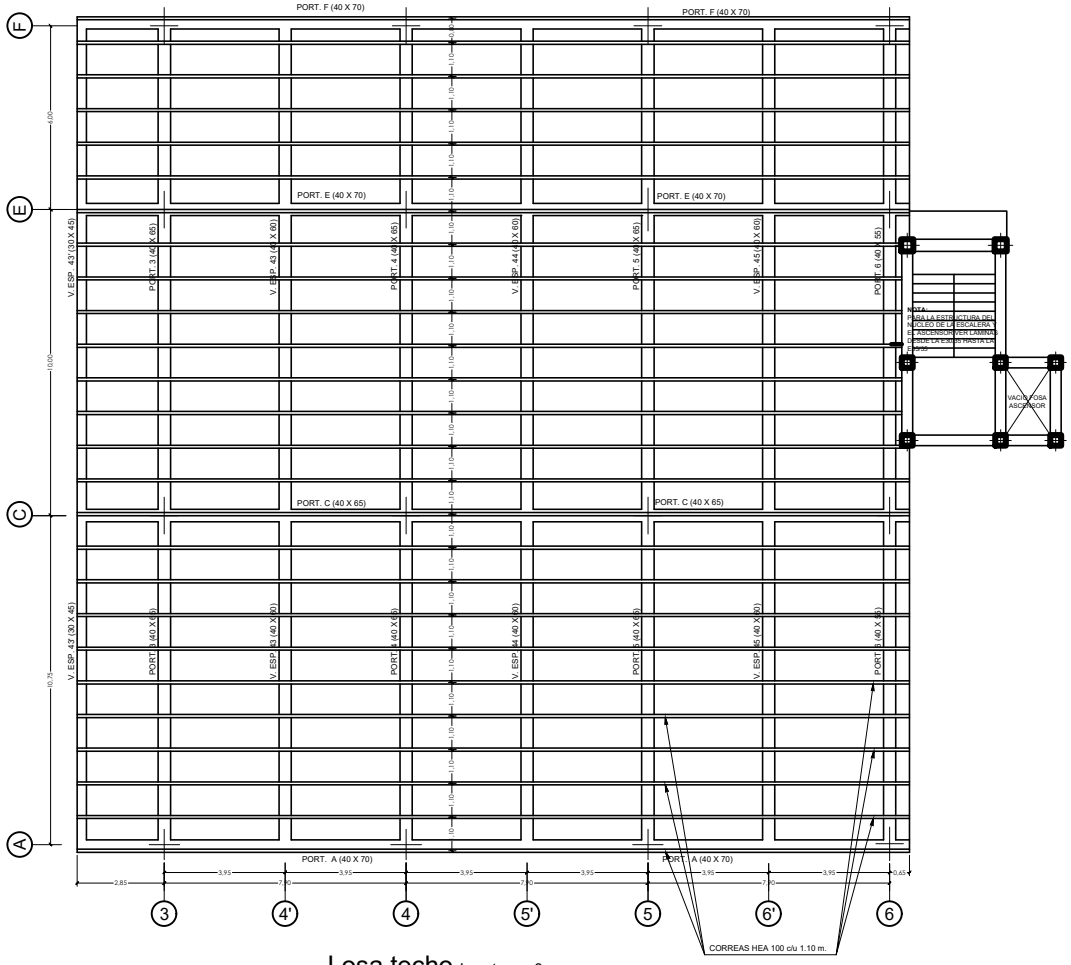


Losa techo Loseta e = 8 cms. Esc. 1: 75


NIVEL (+15.70) (TECHO) (NT)

CORREAS HEA 100 c /u 1.10m

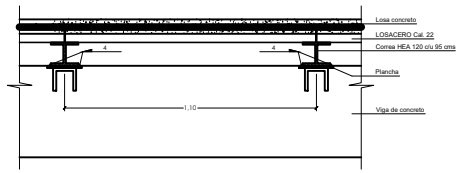


FIJACION LOSACERO ESC. 1:10

Loseta espesor = 8 cms

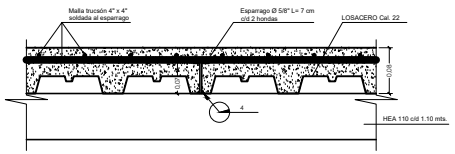

DETALLE LOSACERO ENTREPISO ESC. 1:5


Loseta espesor = 8 cms

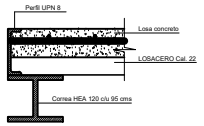

REMATE LATERAL ESC. 1:5

LOSACERO PLANTA TECHO

Espesor = 8 cm, con esparrago Ø 5/8" L = 7 cm.

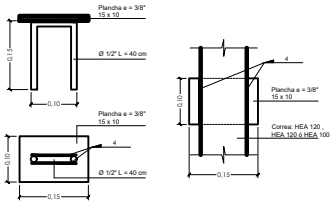

DETALLE PLANCHA ESC. 1:5

PROYECTO: SUPERMERCADO EXPRESS Y OFICINAS CORPORATIVAS

PROPIETARIO: GARZÓN HIPERMERCADO C.A.

UBICACIÓN: AV. PUEBLO NUEVO ANACO, EDO. ANZOATEGUI

PROYECTO: LUZ MARINA C. ARANOVA, C.I.V. 95.596

DIBUJO: OTO

CONTENIDO: ESTRUCTURA LOSA TECHO (NIVEL +15.70 (NT)

N° CATASTRAL: 2023.04.10.0107.01.1.000100.000

FECHA: MARZO, 2011

ESCALA: 1/75

N. DE HOJA:

SERIE: E-11/36

Gregorio H. Garzón James
PROPIETARIO
C.I. 9.218.667

Luz Marina Casanova J.
ARQUITECTO
C.I. V 253.680 C.I.V. 95.596

Gerzón Vivas Rosa
INGENIERO
C.I. 9.207.769 C.I.V. 71.525

Garzón