

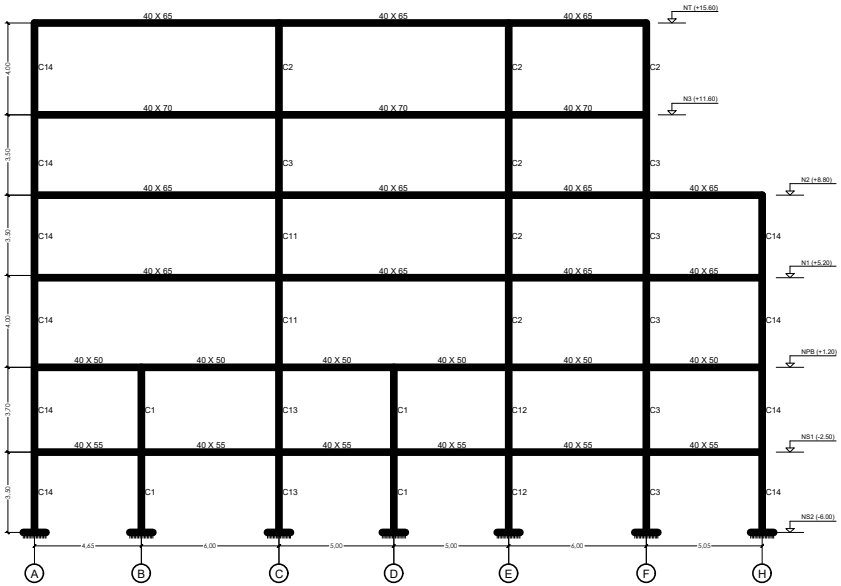



Portico 5

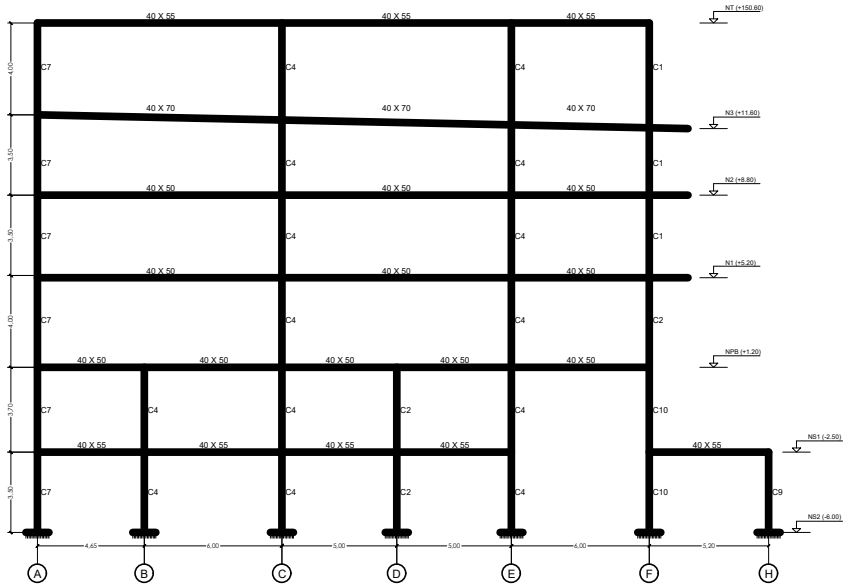


Portico 6

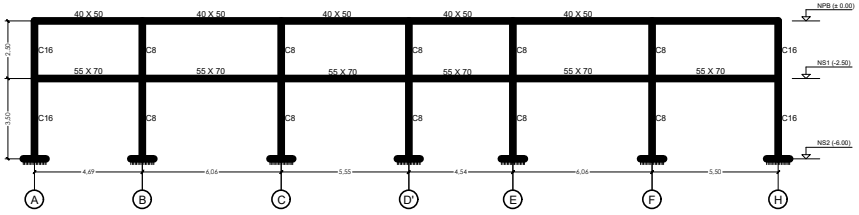

Portico 7

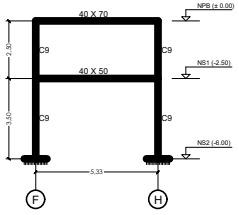

Portico 7'

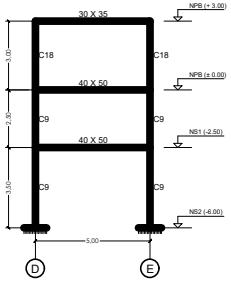

Portico 7''

Gregorio H. Garzón James
PROPIETARIO
C.I. 9.218.667

Luz Marina Casanova J.
ARQUITECTO
C.I. 9.233.680 C.I.V. 95.596

Garzón Vivas Rosa
INGENIERO
C.I. 9.207.769 C.I.V. 71.525

PROYECTO: SUPERMERCADO EXPRESS Y OFICINAS CORPORATIVAS

PROPIETARIO: GARZÓN HIPERMERCADO C.A.
UBICACIÓN: AV. PUEBLO NUEVO ANACO, EDO. ANZOATEGUI
ARQUITECTO: LUZ MARINA CASANOVA
DIBUJO: OTD
FECHA: MARZO 2011
ESCALA: 1/75

CONTENIDO: ESTRUCTURA PORTICO 5, 6, 7, 7' Y 7''
N° CATASTRAL: 2023.04.10.10.007.01.000.000.000

N° DE HOJA:
SERIE: E-27/36