

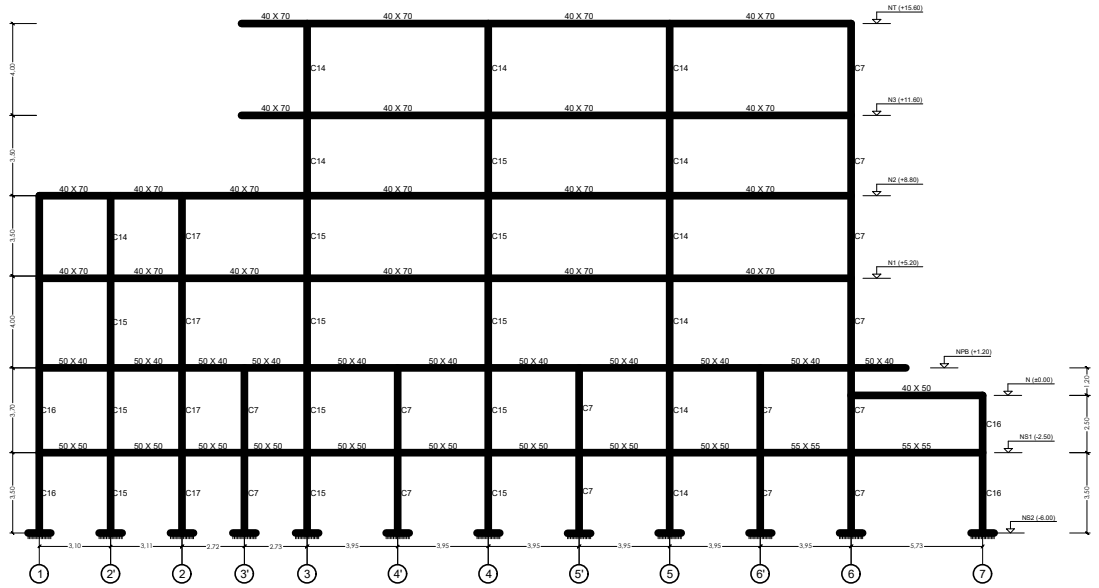



Portico A

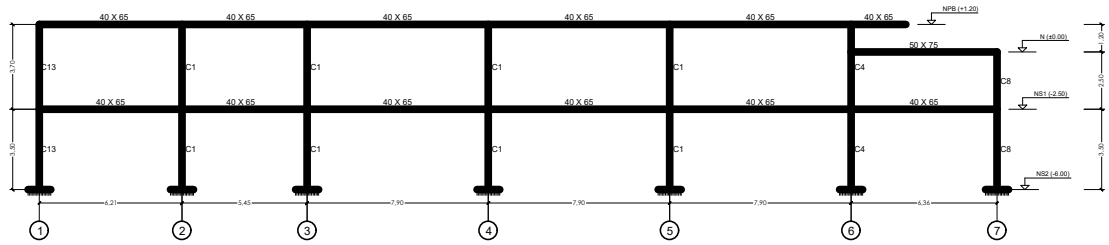

Portico B

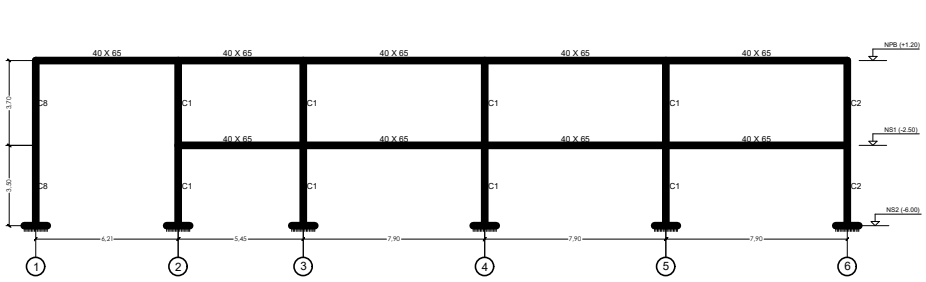

Portico D

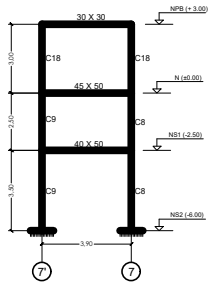

Portico D'

Gregorio H. Garzón James
PROPIETARIO
C.I. 9.218.667

Luz Marina Casanova J.
ARQUITECTO
C.I. 9.253.680 C.I.V. 95.596

Genón Vivas Rosa
INGENIERO
C.I. 9.207.969 C.I.V. 71.525

PROYECTO: SUPERMERCADO EXPRESS Y OFICINAS CORPORATIVAS

PROPIETARIO: GARZÓN HIPERMERCADO C.A.
UBICACIÓN: AV. PUEBLO NUEVO ANACO EDO. ANZOATEGUI
ARQUITECTO: LUZ MARINA CASANOVA C.I.V. 95.596
DIBUJO: OTD

CONTENIDO: ESTRUCTURA PORTICO A, B, D Y D'
N° CATASTRAL: 2023.94.10.10.007.01 1.000.010.000
FECHA: MARZO 2011
ESCALA: 1/75

N° DE HOJA:
SERIE: E-28/36