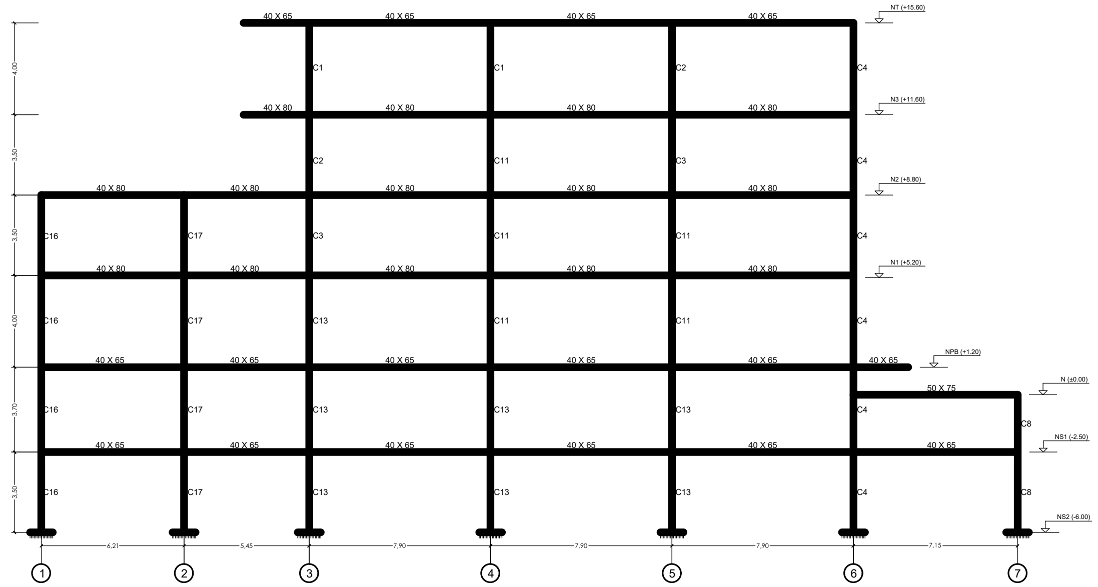

Portico C

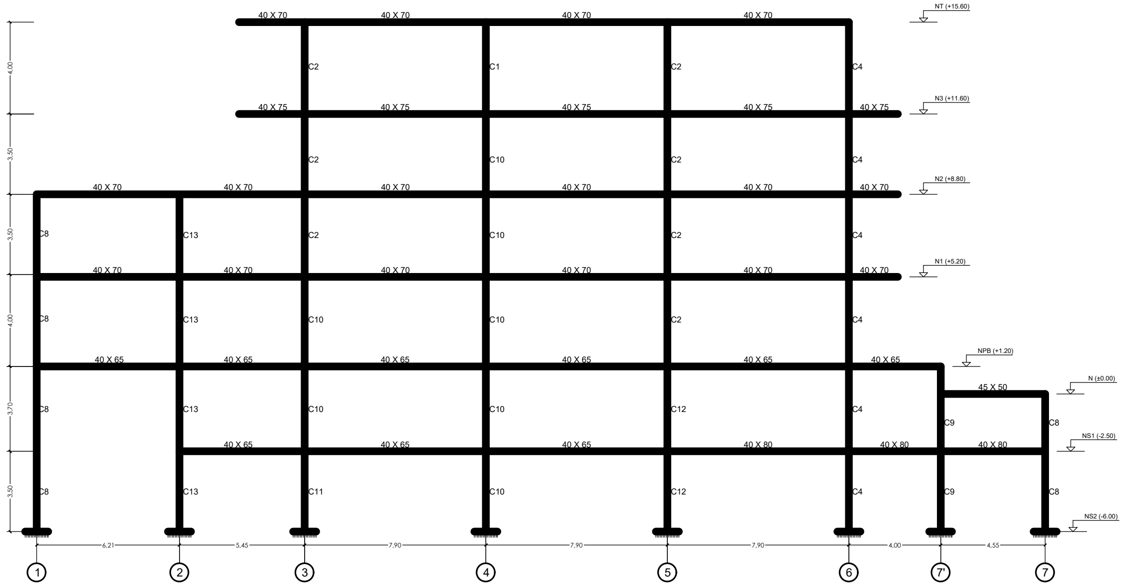

Portico E

Gregorio H. Garzón Jaimes
PROPIETARIO
C.I. 9.218.667

Luz Marina Casanova J.
ARQUITECTO
C.I. 9.233.680 C.I.V. 95.596

Gersón Vivas Roa
INGENIERO
C.I. 9.207.969 C.I.V. 71.525

PROYECTO. SUPERMERCADO EXPRESS Y OFICINAS CORPORATIVAS

PROPIETARIO: GARZÓN HIPERMERCADO C.A.
UBICACION: AV. PUEBLO NUEVO. MUNICIPIO SAN CRISTOBAL. EDO. TACHIRA.
ARQUITECTO: LUZ MARINA CASANOVA. C.I.V. 95.596
CONTENIDO: ESTRUCTURA PORTICO C Y E
N° CATASTRAL: 20-23-04-U01-010-007-011-000-P00-000
DIBUJO: OTTO
FECHA: MARZO 2011
ESCALA: 1/75
No. de Hoja:
SERIE:
E-29/36