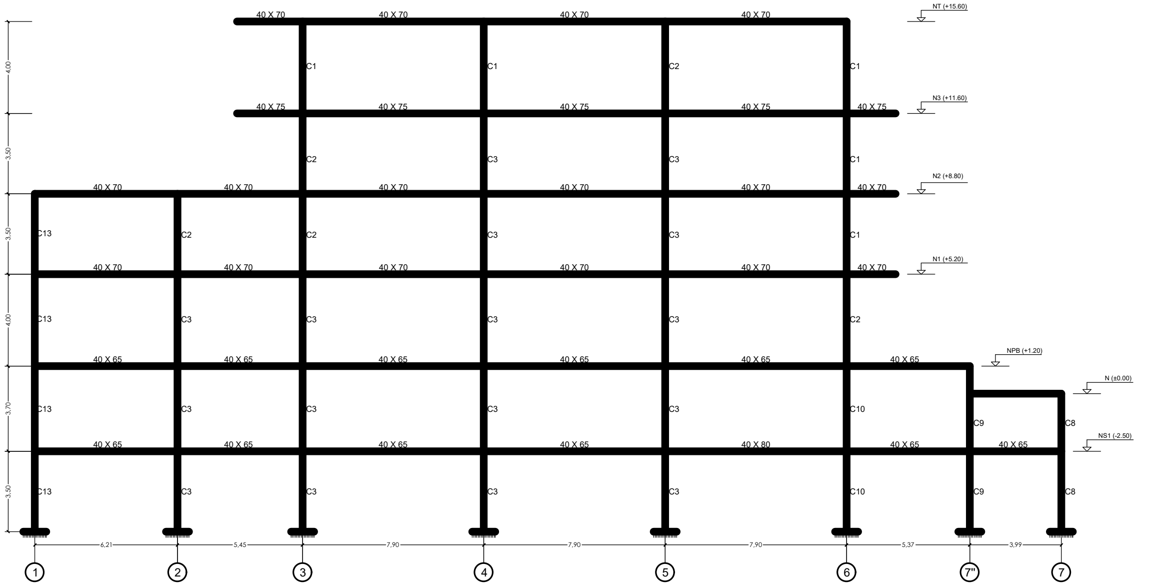

Portico F

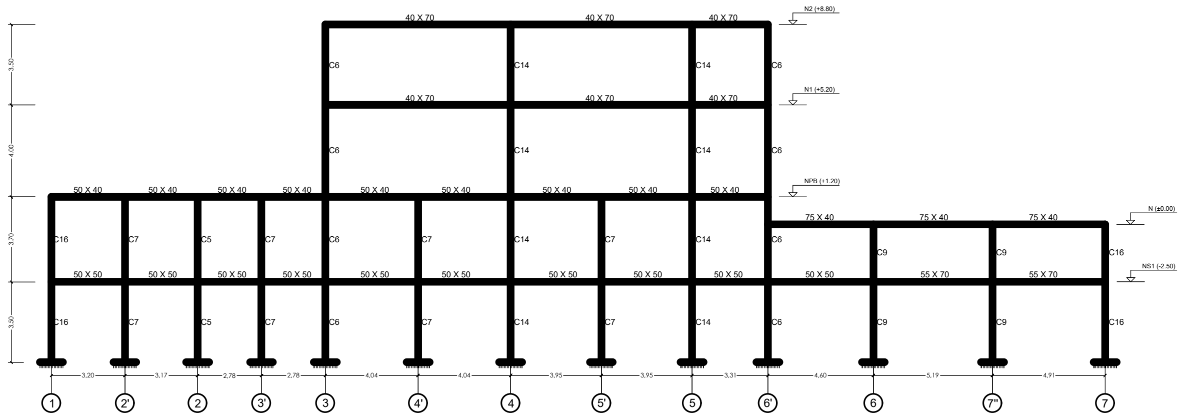

Portico H

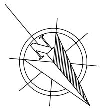

Gregorio H. Garzón Jaimes
PROPIETARIO
C.I. 9.218.667

Luz Marina Casanova J.
ARQUITECTO
C.I. 9.233.680 C.I.V. 95.596

Gersón Vivas Roa
INGENIERO
C.I. 9.207.969 C.I.V. 71.525

No. de Hoja:

SERIE:
E-30/36

PROYECTO. SUPERMERCADO EXPRESS Y OFICINAS CORPORATIVAS

PROPIETARIO:
GARZÓN HIPERMERCADO C.A.

CONTENIDO:
ESTRUCTURA
PORTICO F Y H

UBICACION: AV. PUEBLO NUEVO.
MUNICIPIO SAN CRISTOBAL. EDO. TACHIRA.

Nº CATASTRAL:
20-23-04-U01-010-007-011-000-P00-000

ARQUITECTO:
LUZ MARINA CASANOVA. C.I.V. 95.596

DIBUJO: OTTO

FECHA: MARZO 2011

ESCALA: 1/75

Garzón