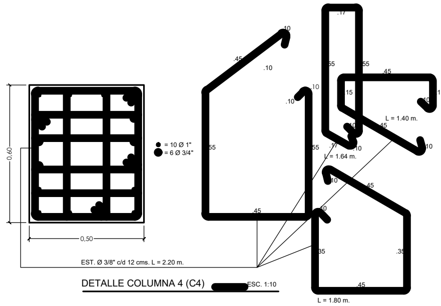
= 10 Ø 1"
= 6 Ø 3/4"
0,60
0,50
EST. Ø 3/8" c/d 12 cms. L = 2.20 m.
L = 1.64 m.
L = 1.40 m.
L = 1.80 m.

DETALLE COLUMNA 4 (C4) ESC. 1:10

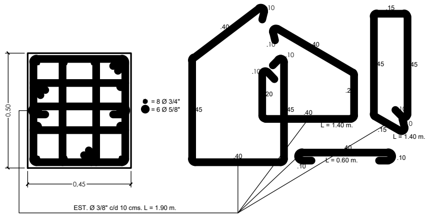
= 8 Ø 3/4"
= 6 Ø 5/8"
0,50
0,45
EST. Ø 3/8" c/d 10 cms. L = 1.90 m.
L = 1.40 m.
L = 1.40 m.
L = 0.60 m.

DETALLE COLUMNA 5 (C5) ESC. 1:10

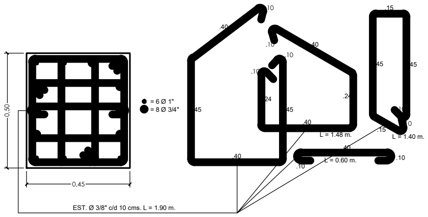
= 6 Ø 1"
= 8 Ø 3/4"
0,50
0,45
EST. Ø 3/8" c/d 10 cms. L = 1.90 m.
L = 1.48 m.
L = 1.40 m.
L = 0.60 m.

DETALLE COLUMNA 6 (C6) ESC. 1:10

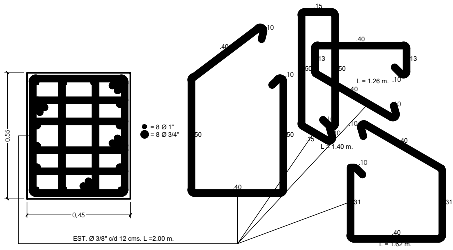
= 8 Ø 1"
= 8 Ø 3/4"
0,55
0,45
EST. Ø 3/8" c/d 12 cms. L =2.00 m.
L = 1.26 m.
L = 1.40 m.
L = 1.62 m.

DETALLE COLUMNA 7 (C7) ESC. 1:10

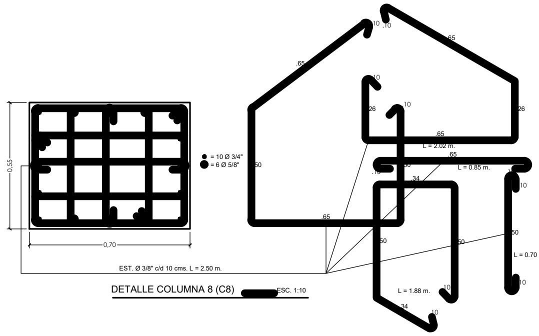
= 10 Ø 3/4"
= 6 Ø 5/8"
0,55
0,70
EST. Ø 3/8" c/d 10 cms. L = 2.50 m.
L = 2.02 m.
L = 0.85 m.
L = 0.70 m.
L = 1.88 m.

DETALLE COLUMNA 8 (C8) ESC. 1:10

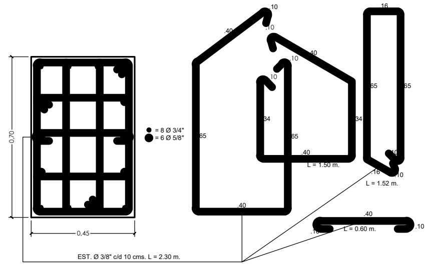
= 8 Ø 3/4"
= 6 Ø 5/8"
0,70
0,45
EST. Ø 3/8" c/d 10 cms. L = 2.30 m.
L = 1.50 m.
L = 1.52 m.
L = 0.60 m.

DETALLE COLUMNA 9 (C9) ESC. 1:10

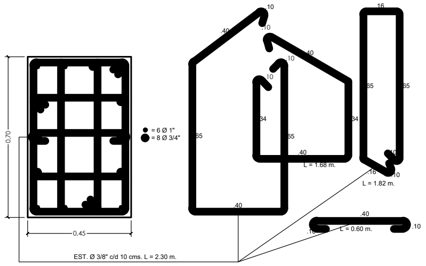
= 6 Ø 1"
= 8 Ø 3/4"
0,70
0,45
EST. Ø 3/8" c/d 10 cms. L = 2.30 m.
L = 1.68 m.
L = 1.82 m.
L = 0.60 m.

DETALLE COLUMNA 10 (C10) ESC. 1:10

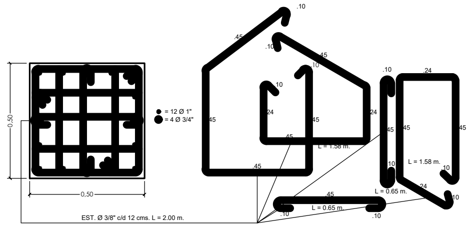
= 12 Ø 1"
= 4 Ø 3/4"
0,50
0,50
EST. Ø 3/8" c/d 12 cms. L = 2.00 m.
L = 1.58 m.
L = 1.58 m.
L = 0.65 m.
L = 0.65 m.

DETALLE COLUMNA 14 (C14) ESC. 1:10

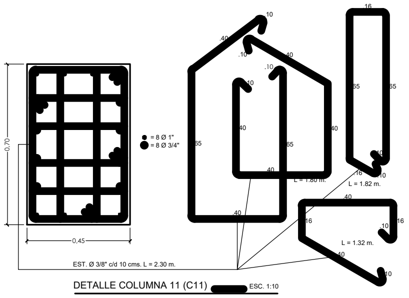
= 8 Ø 1"
= 8 Ø 3/4"
0,70
0,45
EST. Ø 3/8" c/d 10 cms. L = 2.30 m.
L = 1.80 m.
L = 1.82 m.
L = 1.32 m.

DETALLE COLUMNA 11 (C11) ESC. 1:10

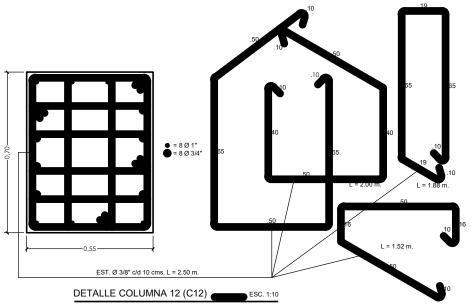
= 8 Ø 1"
= 8 Ø 3/4"
0,70
0,55
EST. Ø 3/8" c/d 10 cms. L = 2.50 m.
L = 2.00 m.
L = 1.88 m.
L = 1.52 m.

DETALLE COLUMNA 12 (C12) ESC. 1:10

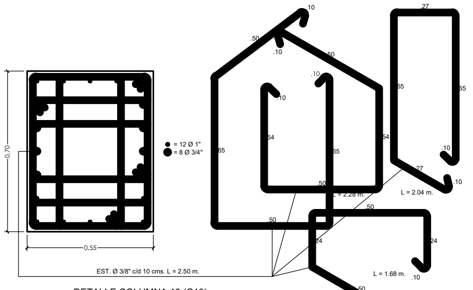
= 12 Ø 1"
= 8 Ø 3/4"
0,70
0,55
EST. Ø 3/8" c/d 10 cms. L = 2.50 m.
L = 2.28 m.
L = 2.04 m.
L = 1.68 m.

DETALLE COLUMNA 13 (C13) ESC. 1:10

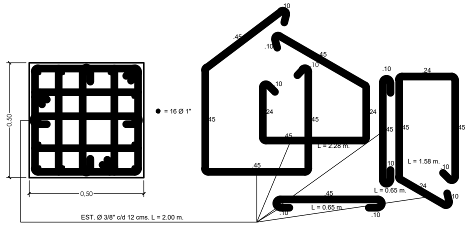
= 16 Ø 1"
0,50
0,50
EST. Ø 3/8" c/d 12 cms. L = 2.00 m.
L = 2.28 m.
L = 1.58 m.
L = 0.65 m.
L = 0.65 m.

DETALLE COLUMNA 15 (C15) ESC. 1:10

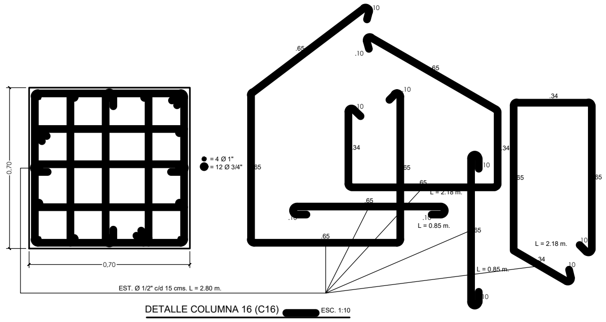
= 4 Ø 1"
= 12 Ø 3/4"
0,70
0,70
EST. Ø 1/2" c/d 15 cms. L = 2.80 m.
L = 2.18 m.
L = 0.85 m.
L = 2.18 m.
L = 0.85 m.

DETALLE COLUMNA 16 (C16) ESC. 1:10

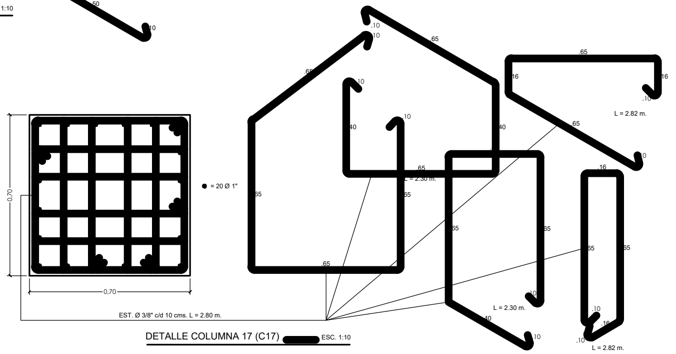
= 20 Ø 1"
0,70
0,70
EST. Ø 3/8" c/d 10 cms. L = 2.80 m.
L = 2.30 m.
L = 2.82 m.
L = 2.30 m.
L = 2.82 m.

DETALLE COLUMNA 17 (C17) ESC. 1:10

Gregorio H. Garzón Jaimes
PROPIETARIO
C.I. 9.218.667

Luz Marina Casanova J.
ARQUITECTO
C.I. 9.233.680 C.I.V. 95.596

Gersón Vivas Roa
INGENIERO
C.I. 9.207.969 C.I.V. 71.525

No. de Hoja:

SERIE:
E-3/36

PROYECTO. SUPERMERCADO EXPRESS
Y OFICINAS CORPORATIVAS

PROPIETARIO: GARZÓN HIPERMERCADO C.A.
UBICACION: AV. PUEBLO NUEVO. MUNICIPIO SAN CRISTOBAL. EDO. TACHIRA.
ARQUITECTO: LUZ MARINA CASANOVA. C.I.V. 95.596
DIBUJO: OTTO
CONTENIDO: ESTRUCTURA COLUMNAS
N° CATASTRAL: 20-23-04-U01-010-007-011-000-P00-000
FECHA: MARZO 2011
ESCALA: 1/10

Garzón