


V. ESP 01 (S1) (40 X 50) (SOTANO 1)

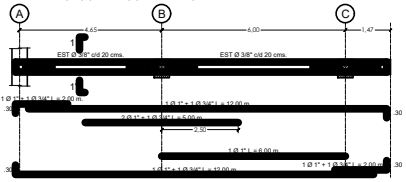


V. ESP 02 (S1) (40 X 50) (SOTANO 1)

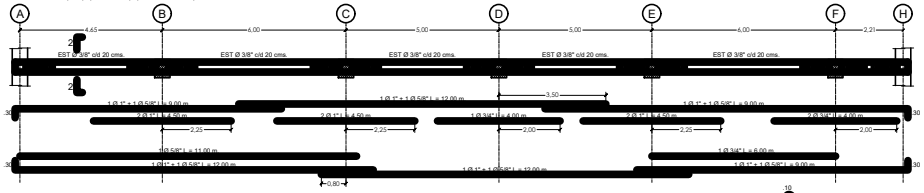


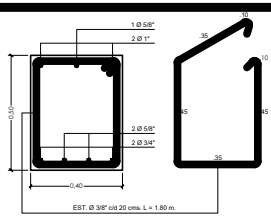


CORTE 1-1' ESC. 1:10

V. ESP 03 (S1) (40 X 50) (SOTANO 1)

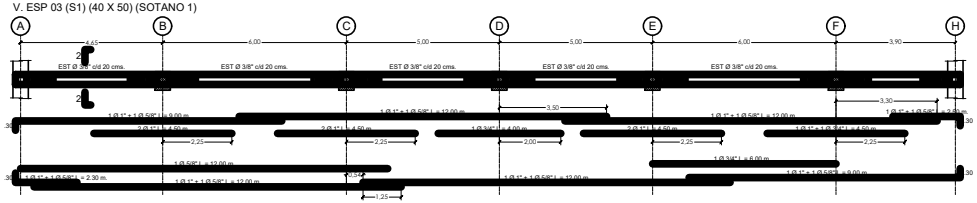


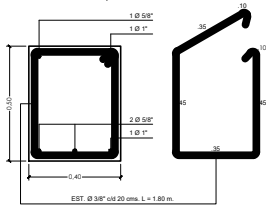

CORTE 2-2' ESC. 1:10

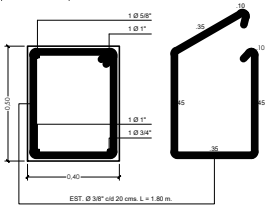


CORTE 3-3' ESC. 1:10

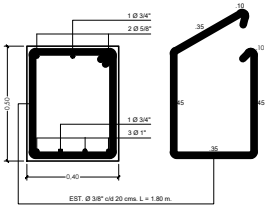


CORTE 4-4' ESC. 1:10


V. ESP 04 (S1) (40 X 50) (SOTANO 1)

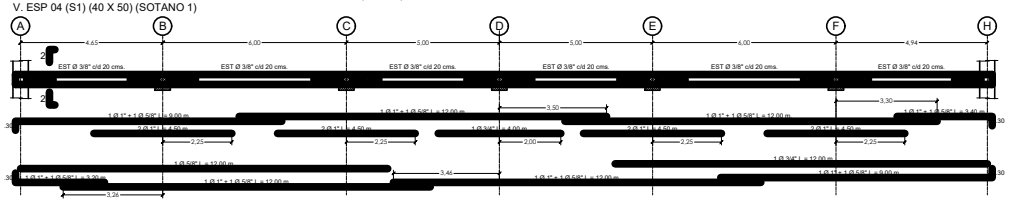


V. ESP 05 (S1) (40 X 50) (SOTANO 1)

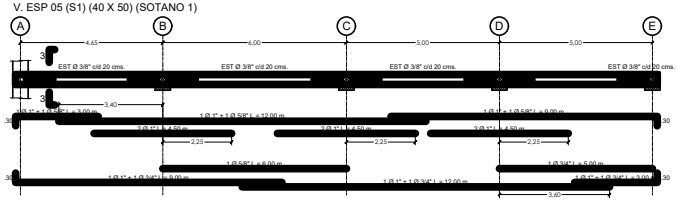


V. ESP 06 (S1) (40 X 50) (SOTANO 1)

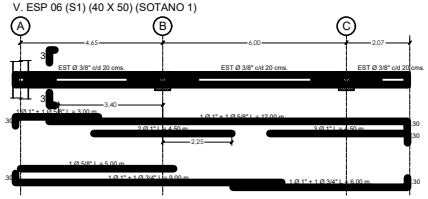


V. ESP 06' (S1) (40 X 50) (SOTANO 1)

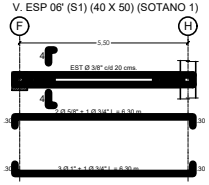


V. ESP 07 (S1) (40 X 50) (SOTANO 1)

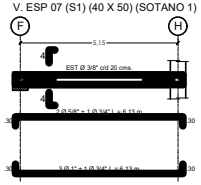


V. ESP 46 (S1) (40 X 60) (SOTANO 1) (RAMPA ACCESO)

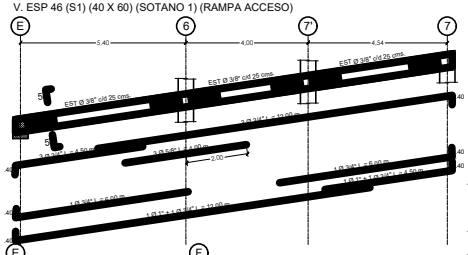


V. ESP 47 (S1) (40 X 60) (SOTANO 1) (RAMPA ACCESO)

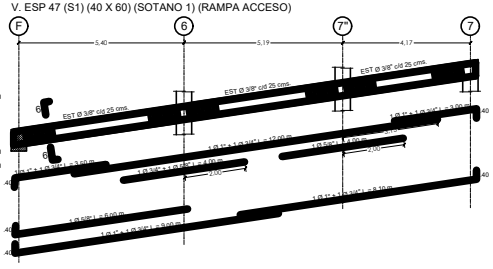


V. ESP 48 (S1) (40 X 50) (SOTANO 1)

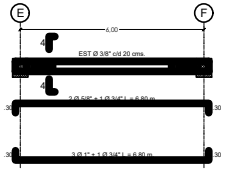


V. ESP 09 (PB) (40 X 45) (PLANTA BAJA)

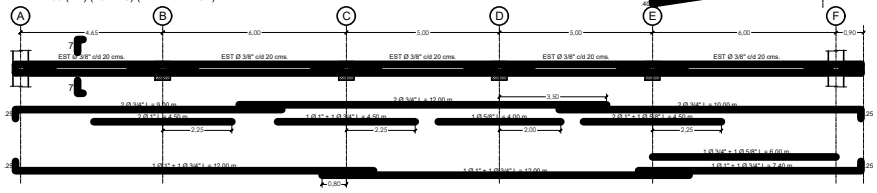


V. ESP 10 (PB) (40 X 45) (PLANTA BAJA)

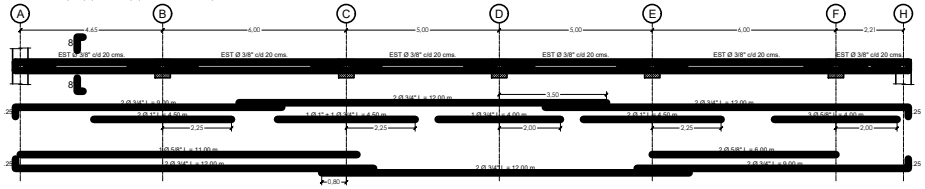


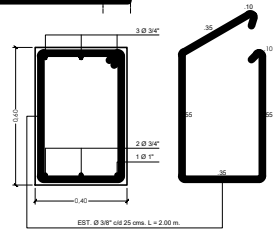

CORTE 5-5' ESC. 1:10

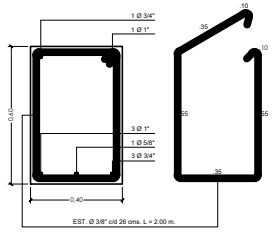

CORTE 6-6' ESC. 1:10

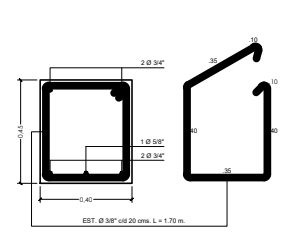

CORTE 8-8' ESC. 1:10

Gregorio H. Garzón James
PROPIETARIO
C.I. 9.218.667

Luz Marina Casanova J.
ARQUITECTO
C.I. 9.233.680 C.I.V. 95.596

Carolin Vivas Rosa
INGENIERO
C.I. 9.207.769 C.I.V. 71.525

PROYECTO: SUPERMERCADO EXPRESS Y OFICINAS CORPORATIVAS

PROPIETARIO: GARZÓN HIPERMERCADO C.A.
UBICACIÓN: AV. PUEBLO NUEVO
ARQUITECTURA Y CONSTRUCCIÓN VIAL, EDO. TÁCHIRA

CONTENIDO: ESTRUCTURA VIGAS ESPECIALES

PROYECTO: LUZ MARINA C.A.NOVA, C.I.V. 95.596

DIBUJO: OTD

FECHA: MARZO 2011

ESCALA: 1/75

N° CATASTRAL: 2023.04.10.10.007.01.1.000.000.000

N° DE HOJA:

SERIE: E-12/36

Garzón