V. ESP 20 (PB) (40 X 50) (PLANTA BAJA)
NIVEL ± 0.00

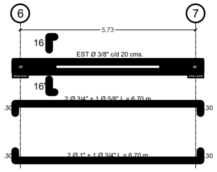

V. ESP 20' (PB) (35 X 40) (PTA. BAJA)
NIVEL ± 0.00

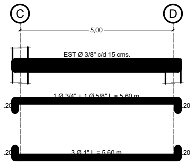

V. ESP 21 (PB) (50 X 75) (PLANTA BAJA)
NIVEL ± 0.00

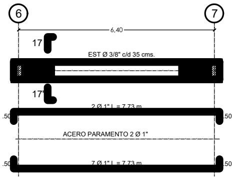

V. ESP 22 (PB) (50 X 75) (PLANTA BAJA)
NIVEL ± 0.00

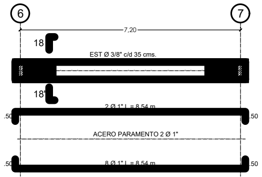

V. ESP 23 (PB) (45 X 50)
(PLANTA BAJA) NIVEL ± 0.00

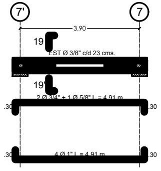

V. ESP 24 (PB) (45 X 50)
(PLANTA BAJA) NIVEL ± 0.00

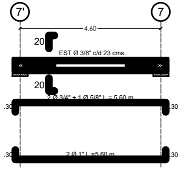

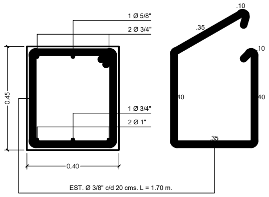

CORTE 16-16' [redacted] ESC. 1:10

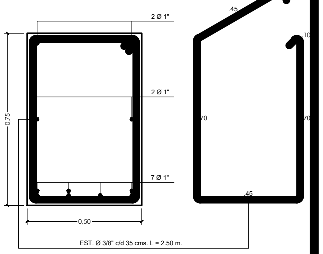

CORTE 17-17' [redacted] ESC. 1:10

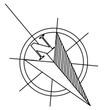

V. ESP 25 (N1) (30 X 40) (1° PISO)

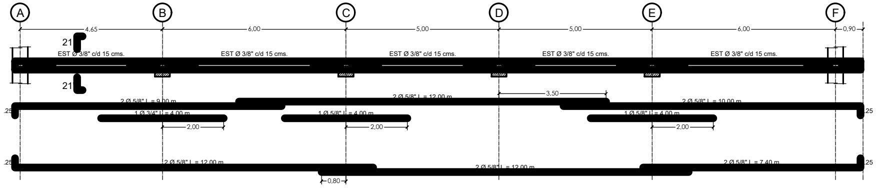

V. ESP 26 (N1) (40 X 70) (1° PISO)

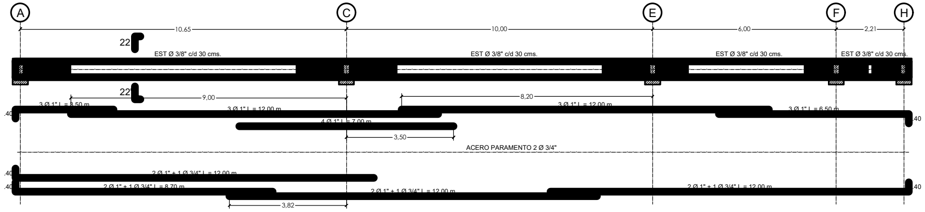

V. ESP 27 (N1) (40 X 70) (1° PISO)

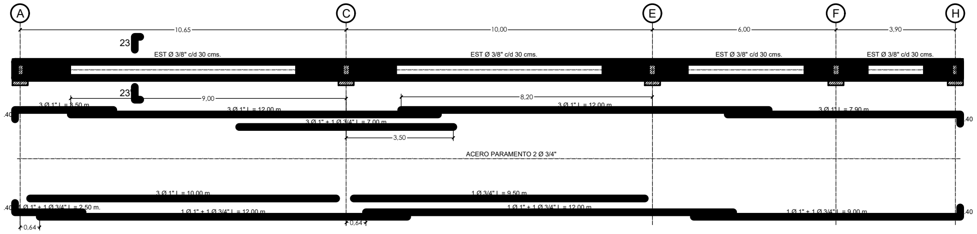

V. ESP 28 = V. ESP. 29 (N1) (40 X 65) (1° PISO)

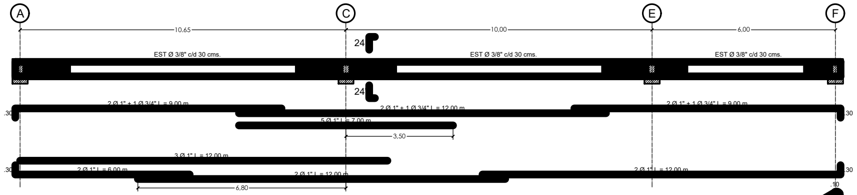

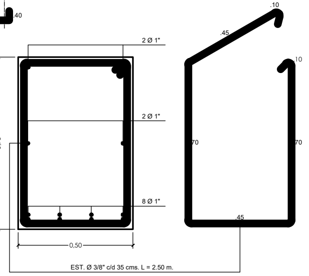

CORTE 18-18' [redacted] ESC. 1:10

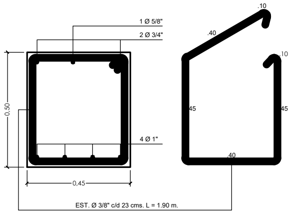

CORTE 19-19' [redacted] ESC. 1:10

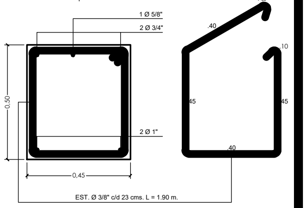

CORTE 20-20' [redacted] ESC. 1:10

V. ESP 30 (N1) (25 X 35)
(1° PISO)

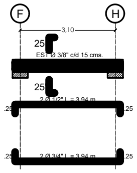

V. ESP 31 (N1) (30 X 45) (1° PISO)

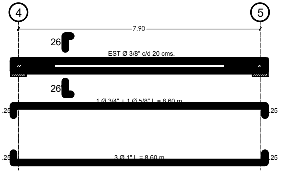

V. ESP 32 (N1) (30 X 35) (1° PISO)

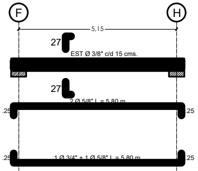

V. ESP 32' (N1) (25 X 35) (1° PISO)

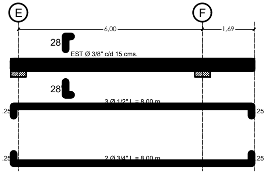

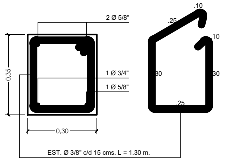

CORTE 27-27' [redacted] ESC. 1:10

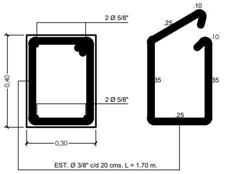

CORTE 21-21' [redacted] ESC. 1:10

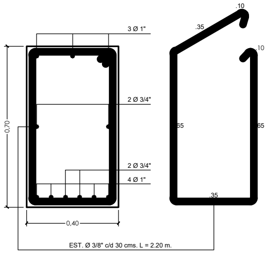

CORTE 22-22' [redacted] ESC. 1:10

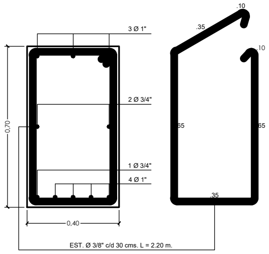

CORTE 23-23' [redacted] ESC. 1:10

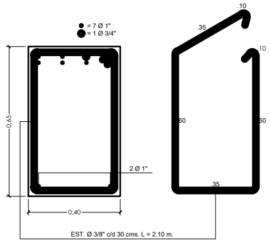

CORTE 24-24' [redacted] ESC. 1:10

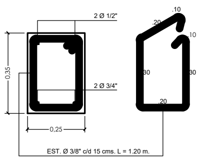

CORTE 25-25' [redacted] ESC. 1:10

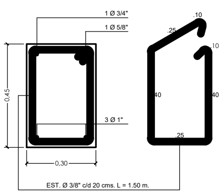

CORTE 26-26' [redacted] ESC. 1:10

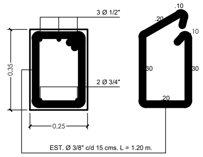

CORTE 28-28' [redacted] ESC. 1:10

Gregorio H. Garzón Jaimes
PROPIETARIO
C.I. 9.218.667

Luz Marina Casanova J.
ARQUITECTO
C.I. 9.233.680 C.I.V. 95.596

Gersón Vivas Roa
INGENIERO
C.I. 9.207.969 C.I.V. 71.525

No. de Hoja:

SERIE:
E-14/36

PROYECTO. SUPERMERCADO EXPRESS Y OFICINAS CORPORATIVAS

PROPIETARIO: GARZÓN HIPERMERCADO C.A.
UBICACION: AV. PUEBLO NUEVO. MUNICIPIO SAN CRISTOBAL. EDO. TACHIRA.
ARQUITECTO: LUZ MARINA CASANOVA. C.I.V. 95.596
DIBUJO: OTTO
CONTENIDO: ESTRUCTURA VIGAS ESPECIALES
N° CATASTRAL: 20-23-04-U01-010-007-011-000-P00-000
FECHA: MARZO 2011
ESCALA: 1/75